


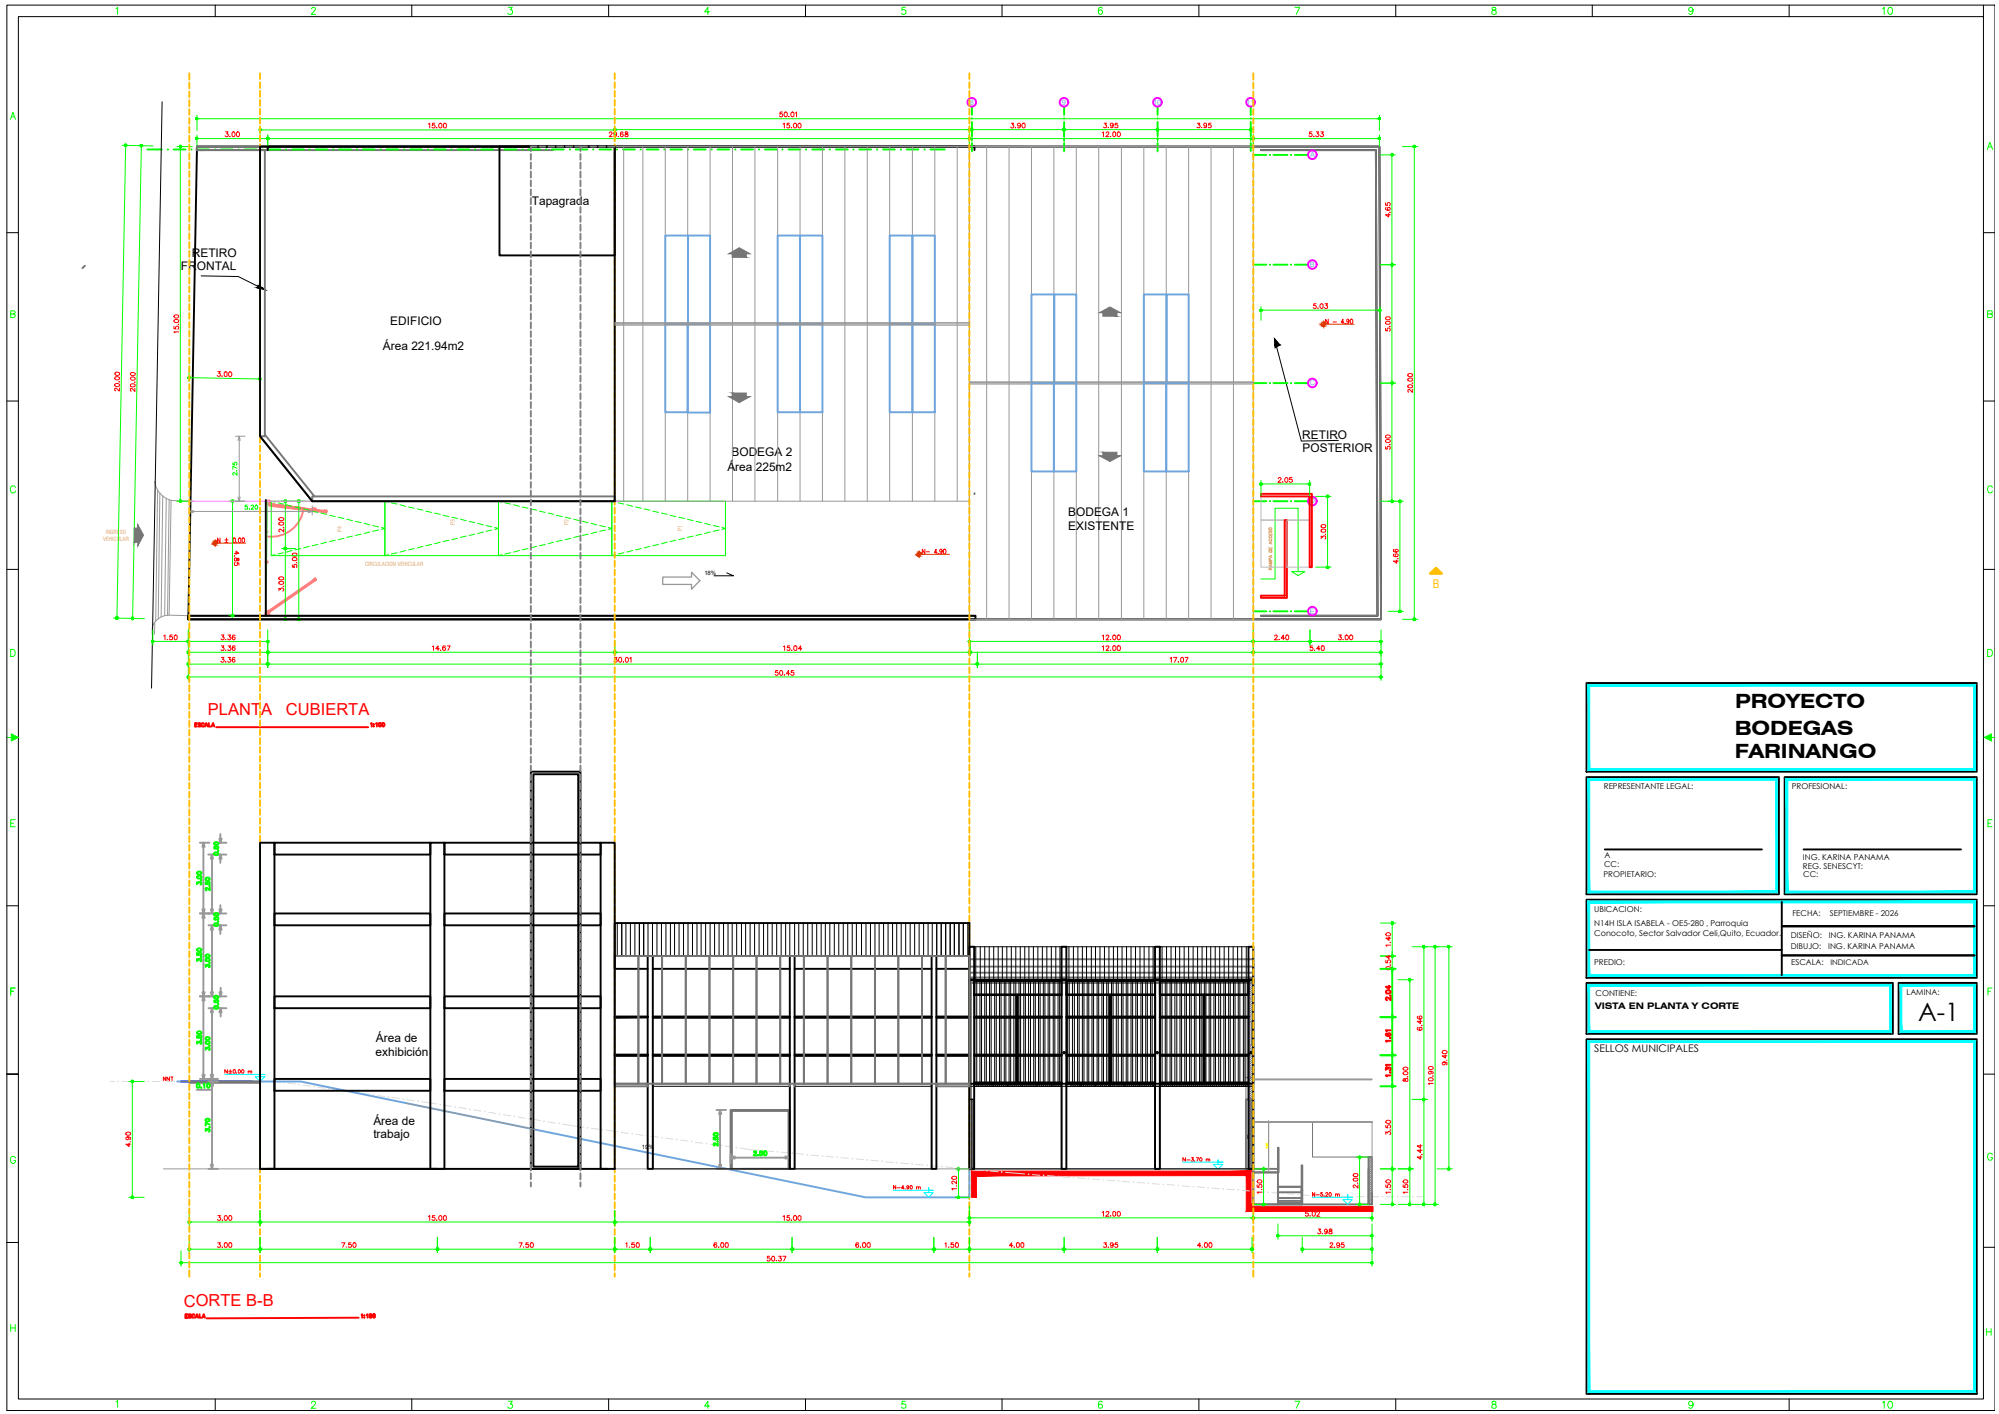

PROYECTO BODEGAS FARINANGO	
REPRESENTANTE LEGAL: A CC: PROPIETARIO:	PROFESIONAL: ING. KARINA PANAMA REG. SENESCYT: CC:
UBICACION: N14H ISLA ISABELA - OES-280, Parroquia Coronado, Sector Salvador Cel. Quito, Ecuador	FECHA: SEPTIEMBRE - 2024 DISEÑO: ING. KARINA PANAMA DIBUJO: ING. KARINA PANAMA ESCALA: INDICADA
CONTIENE: VISTA EN PLANTA Y CORTE	LÁMINA: A-1
SELLOS MUNICIPALES	