


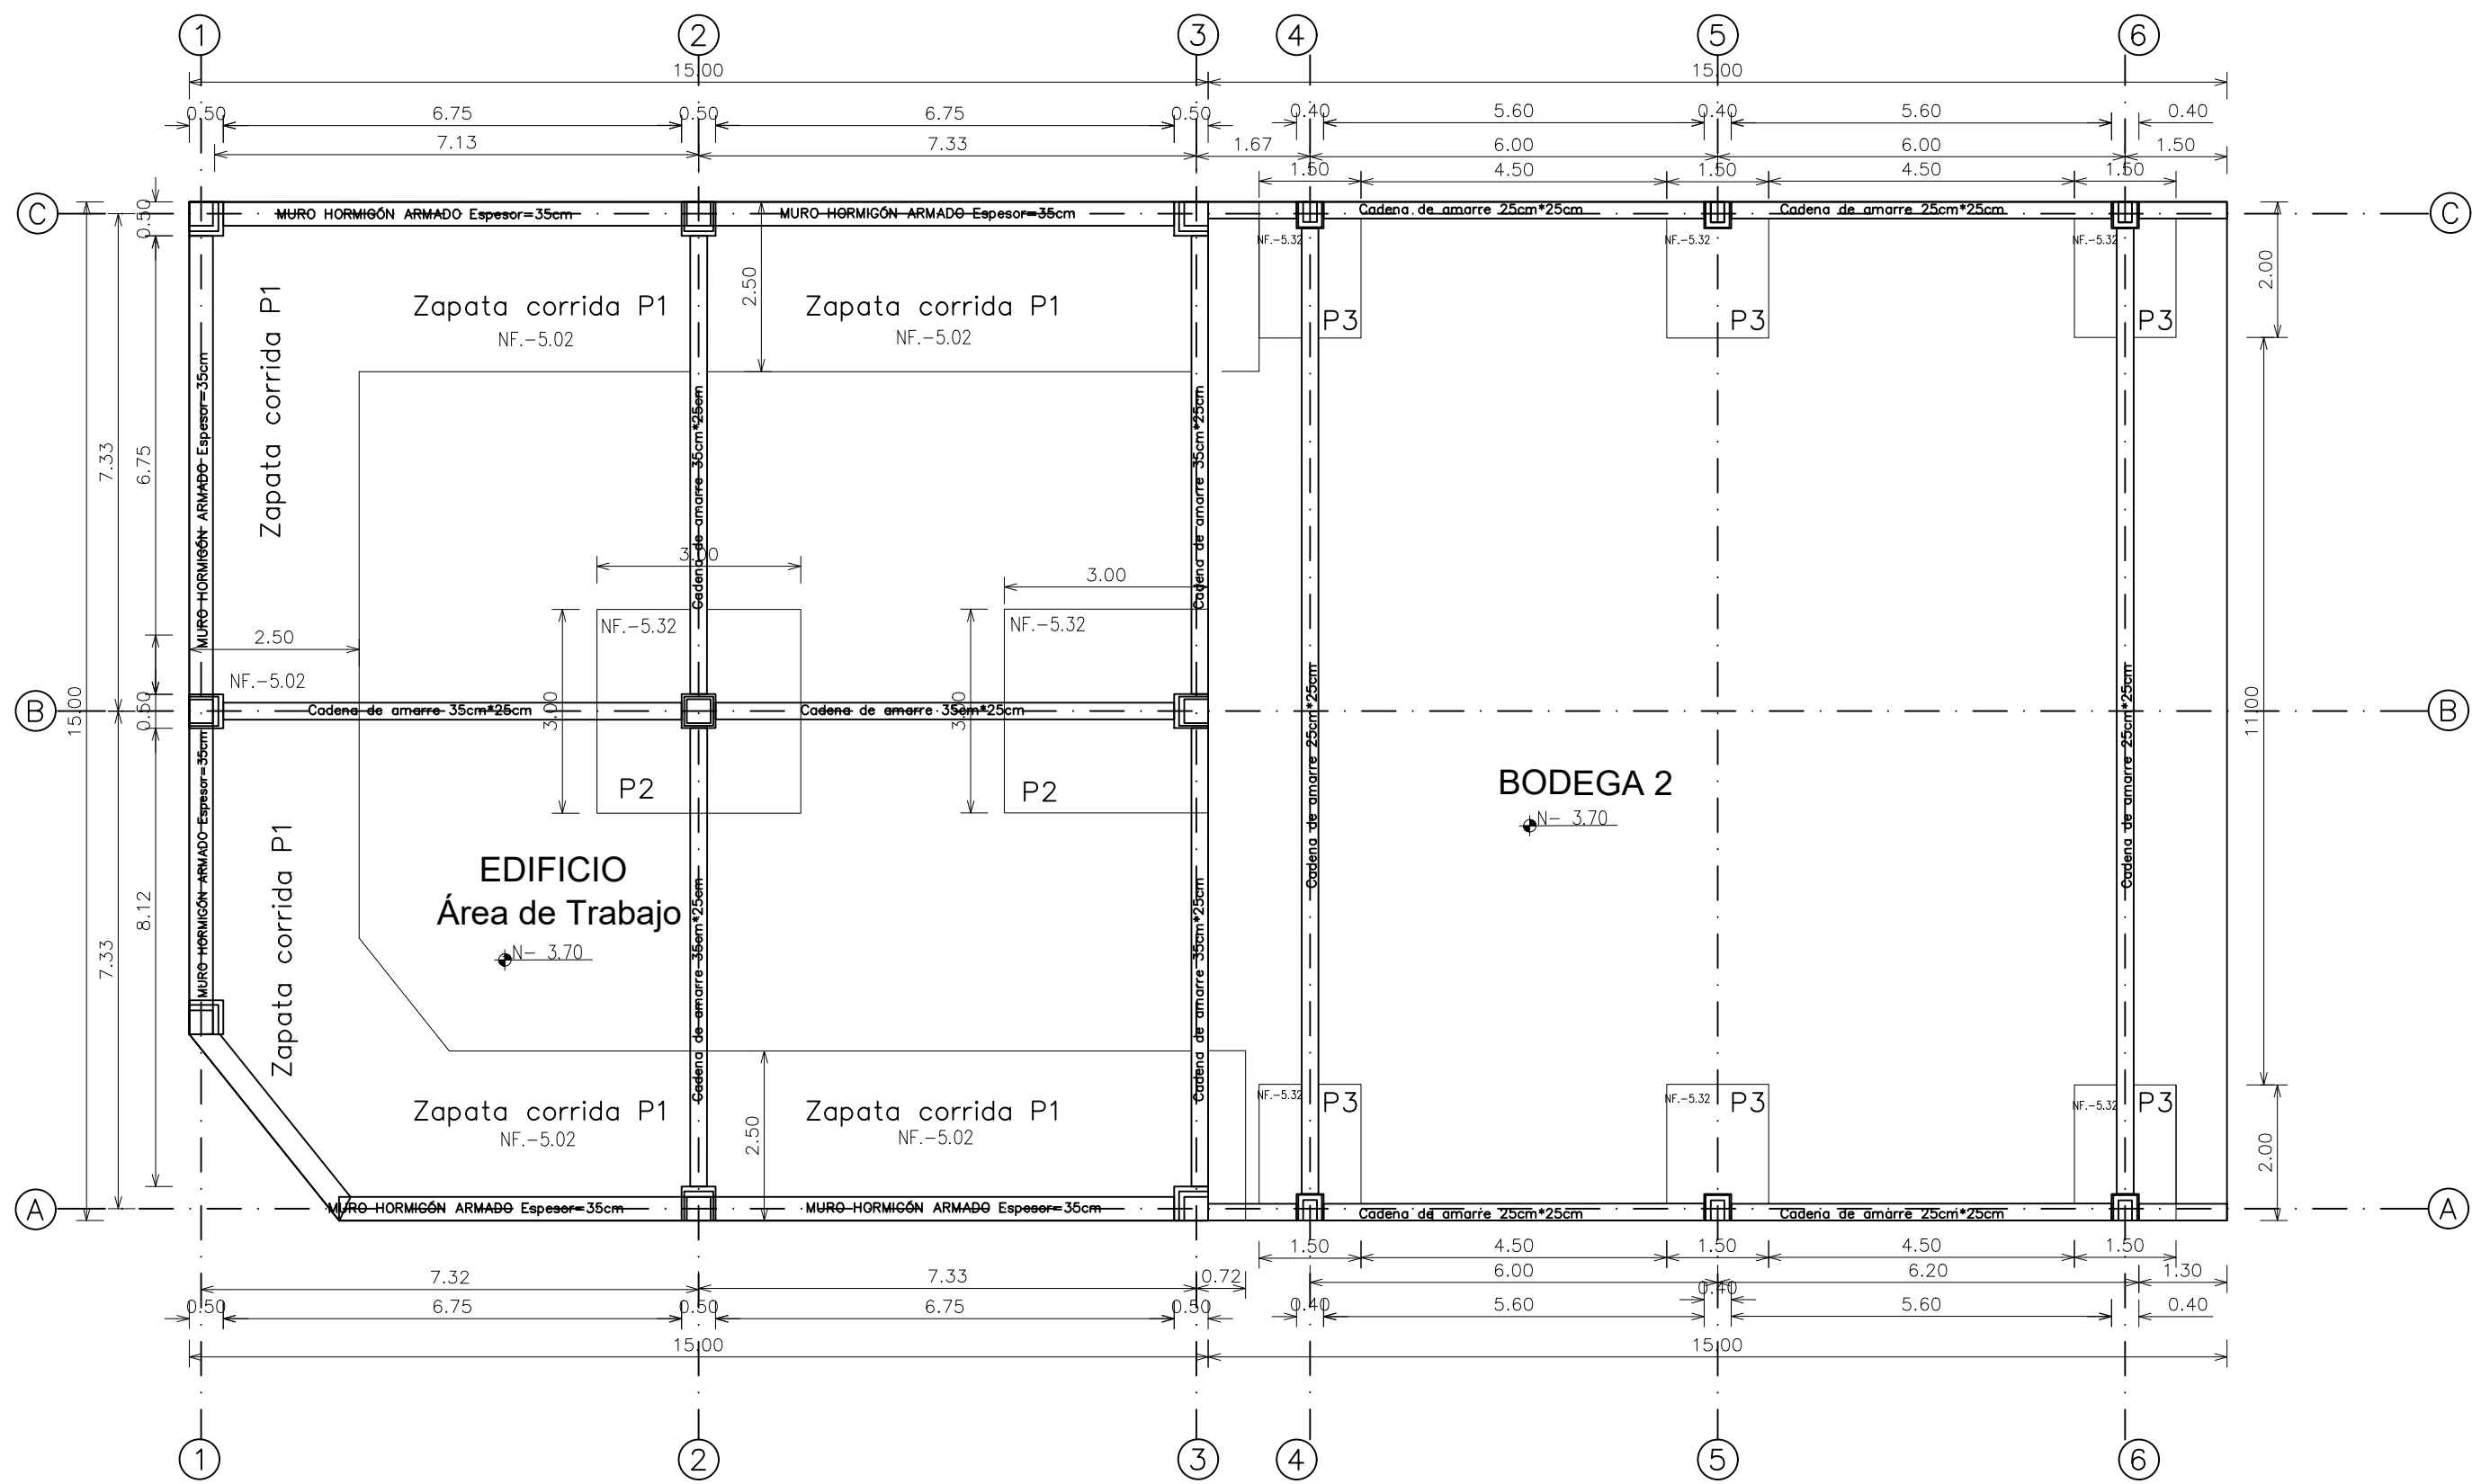


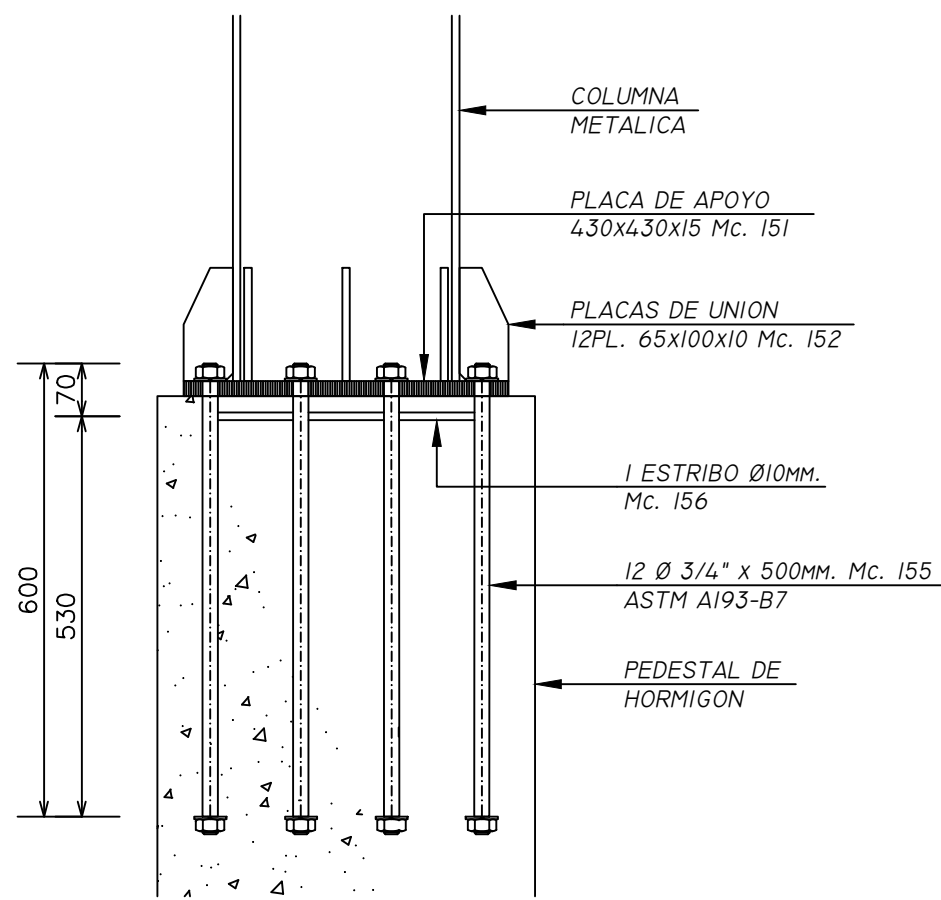


PLANTA CIMENTACIÓN
Escala 1:100

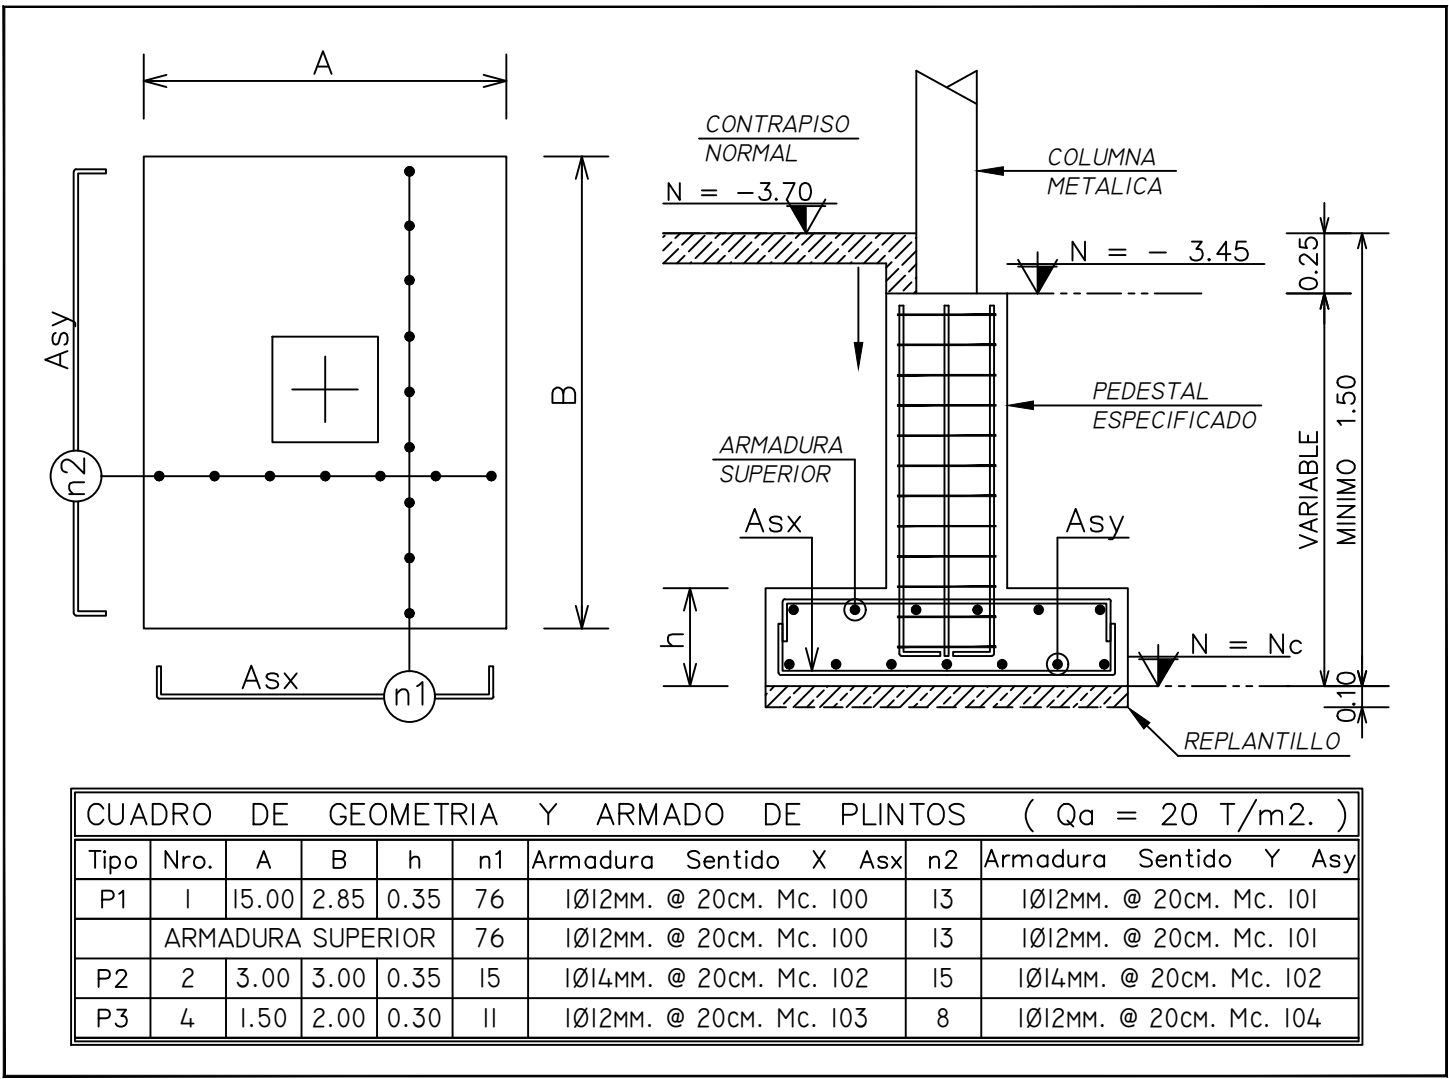


ELEVACION TIPICA DE CANASTILLAS
Escala 1:10

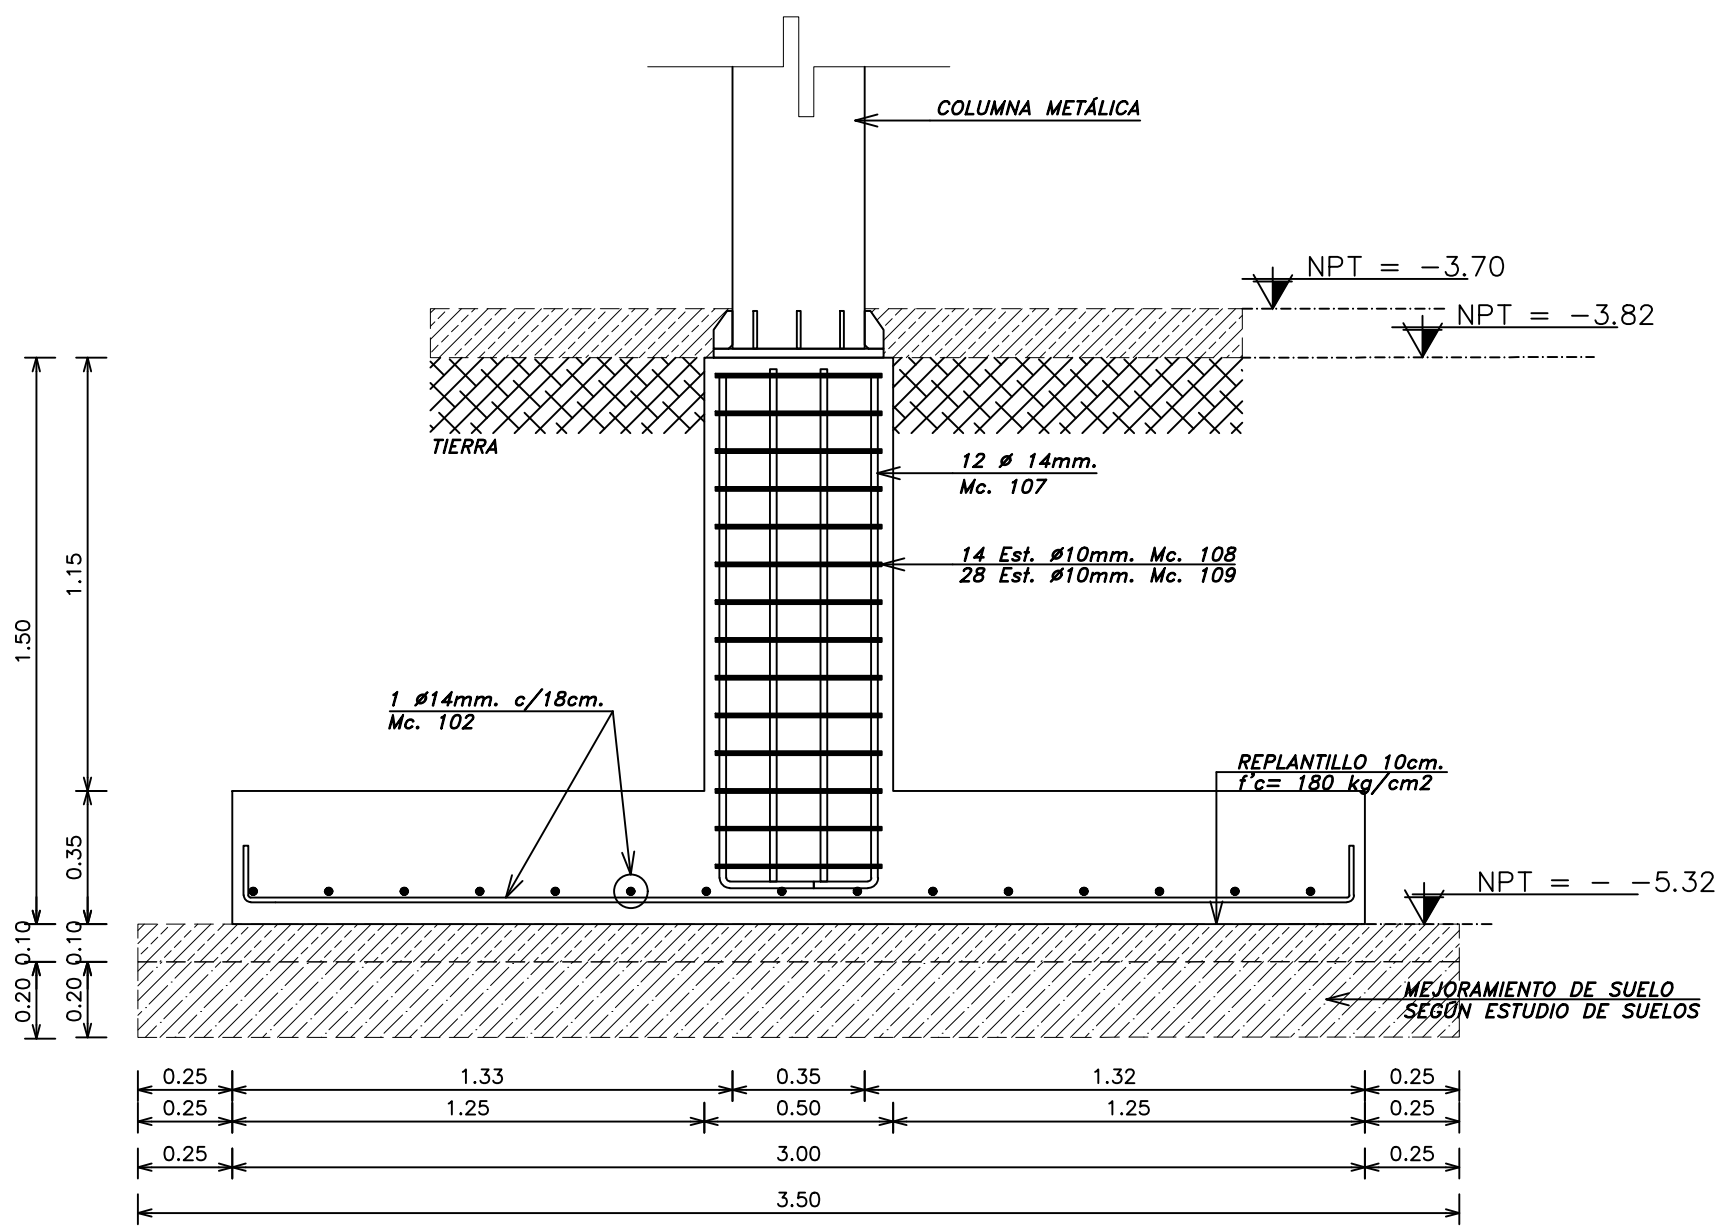


DETALLE DE ELEVACIÓN DE CIMENTACIÓN P2 (2 unidades)
Escala 1:20

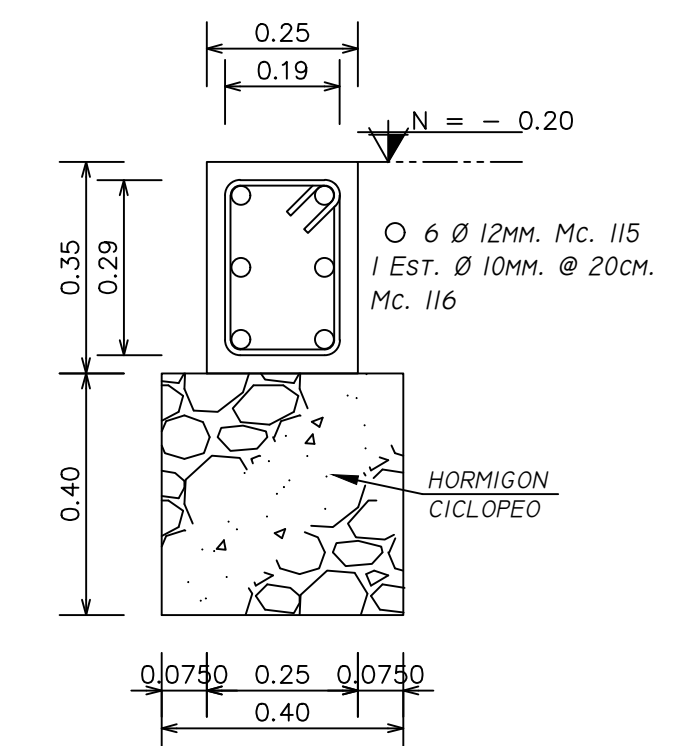


DETALLE DE CADENA CORTE 1-1
Escala 1:12.5

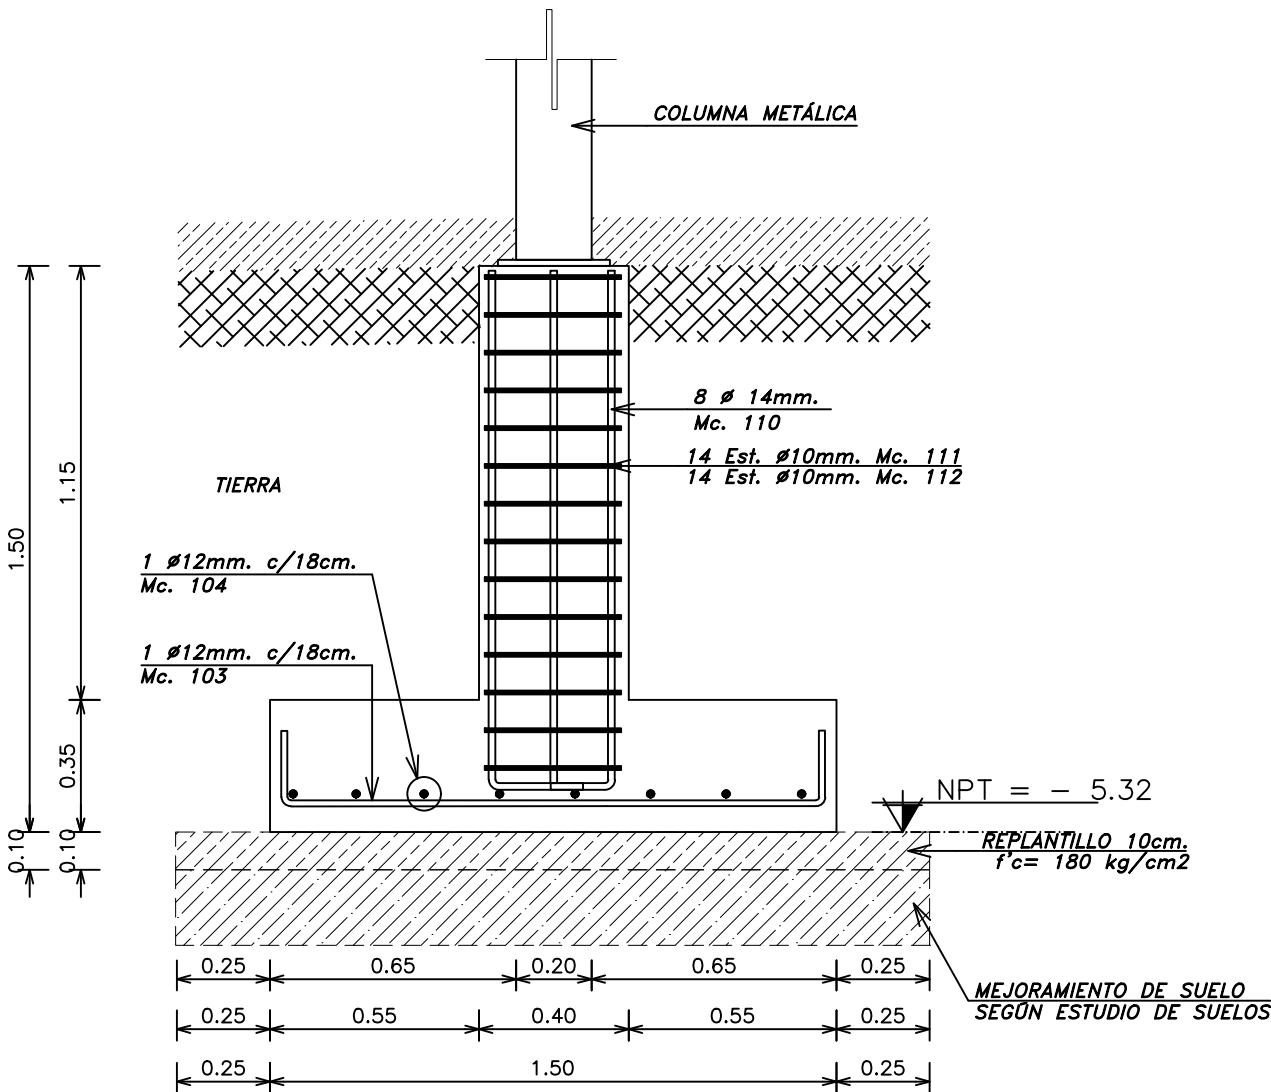


DETALLE DE ELEVACIÓN DE CIMENTACIÓN P3 (6 unidades)
Escala 1:20

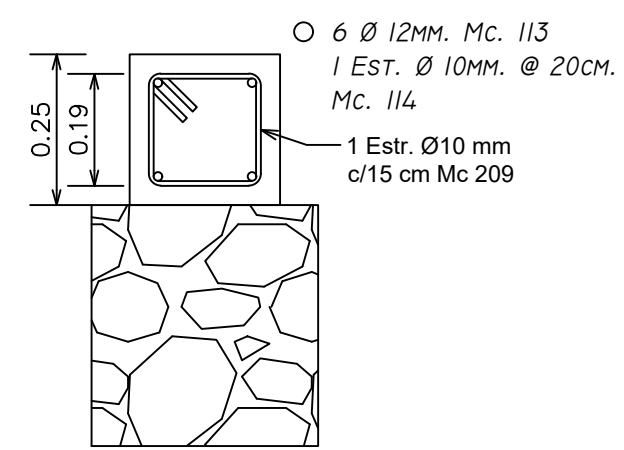

DETALLE DE CADENA CORTE 2-2
Escala 1:12.5

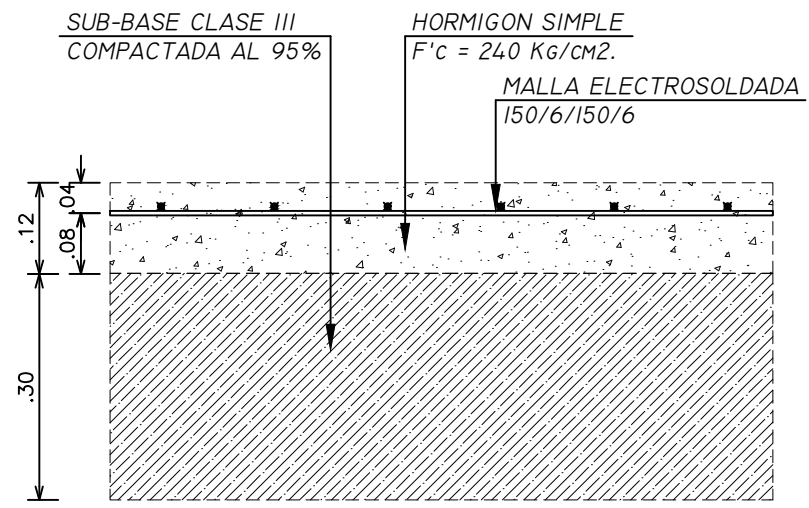

DETALLE DE CONTRAPISO NORMAL
Escala 1:10

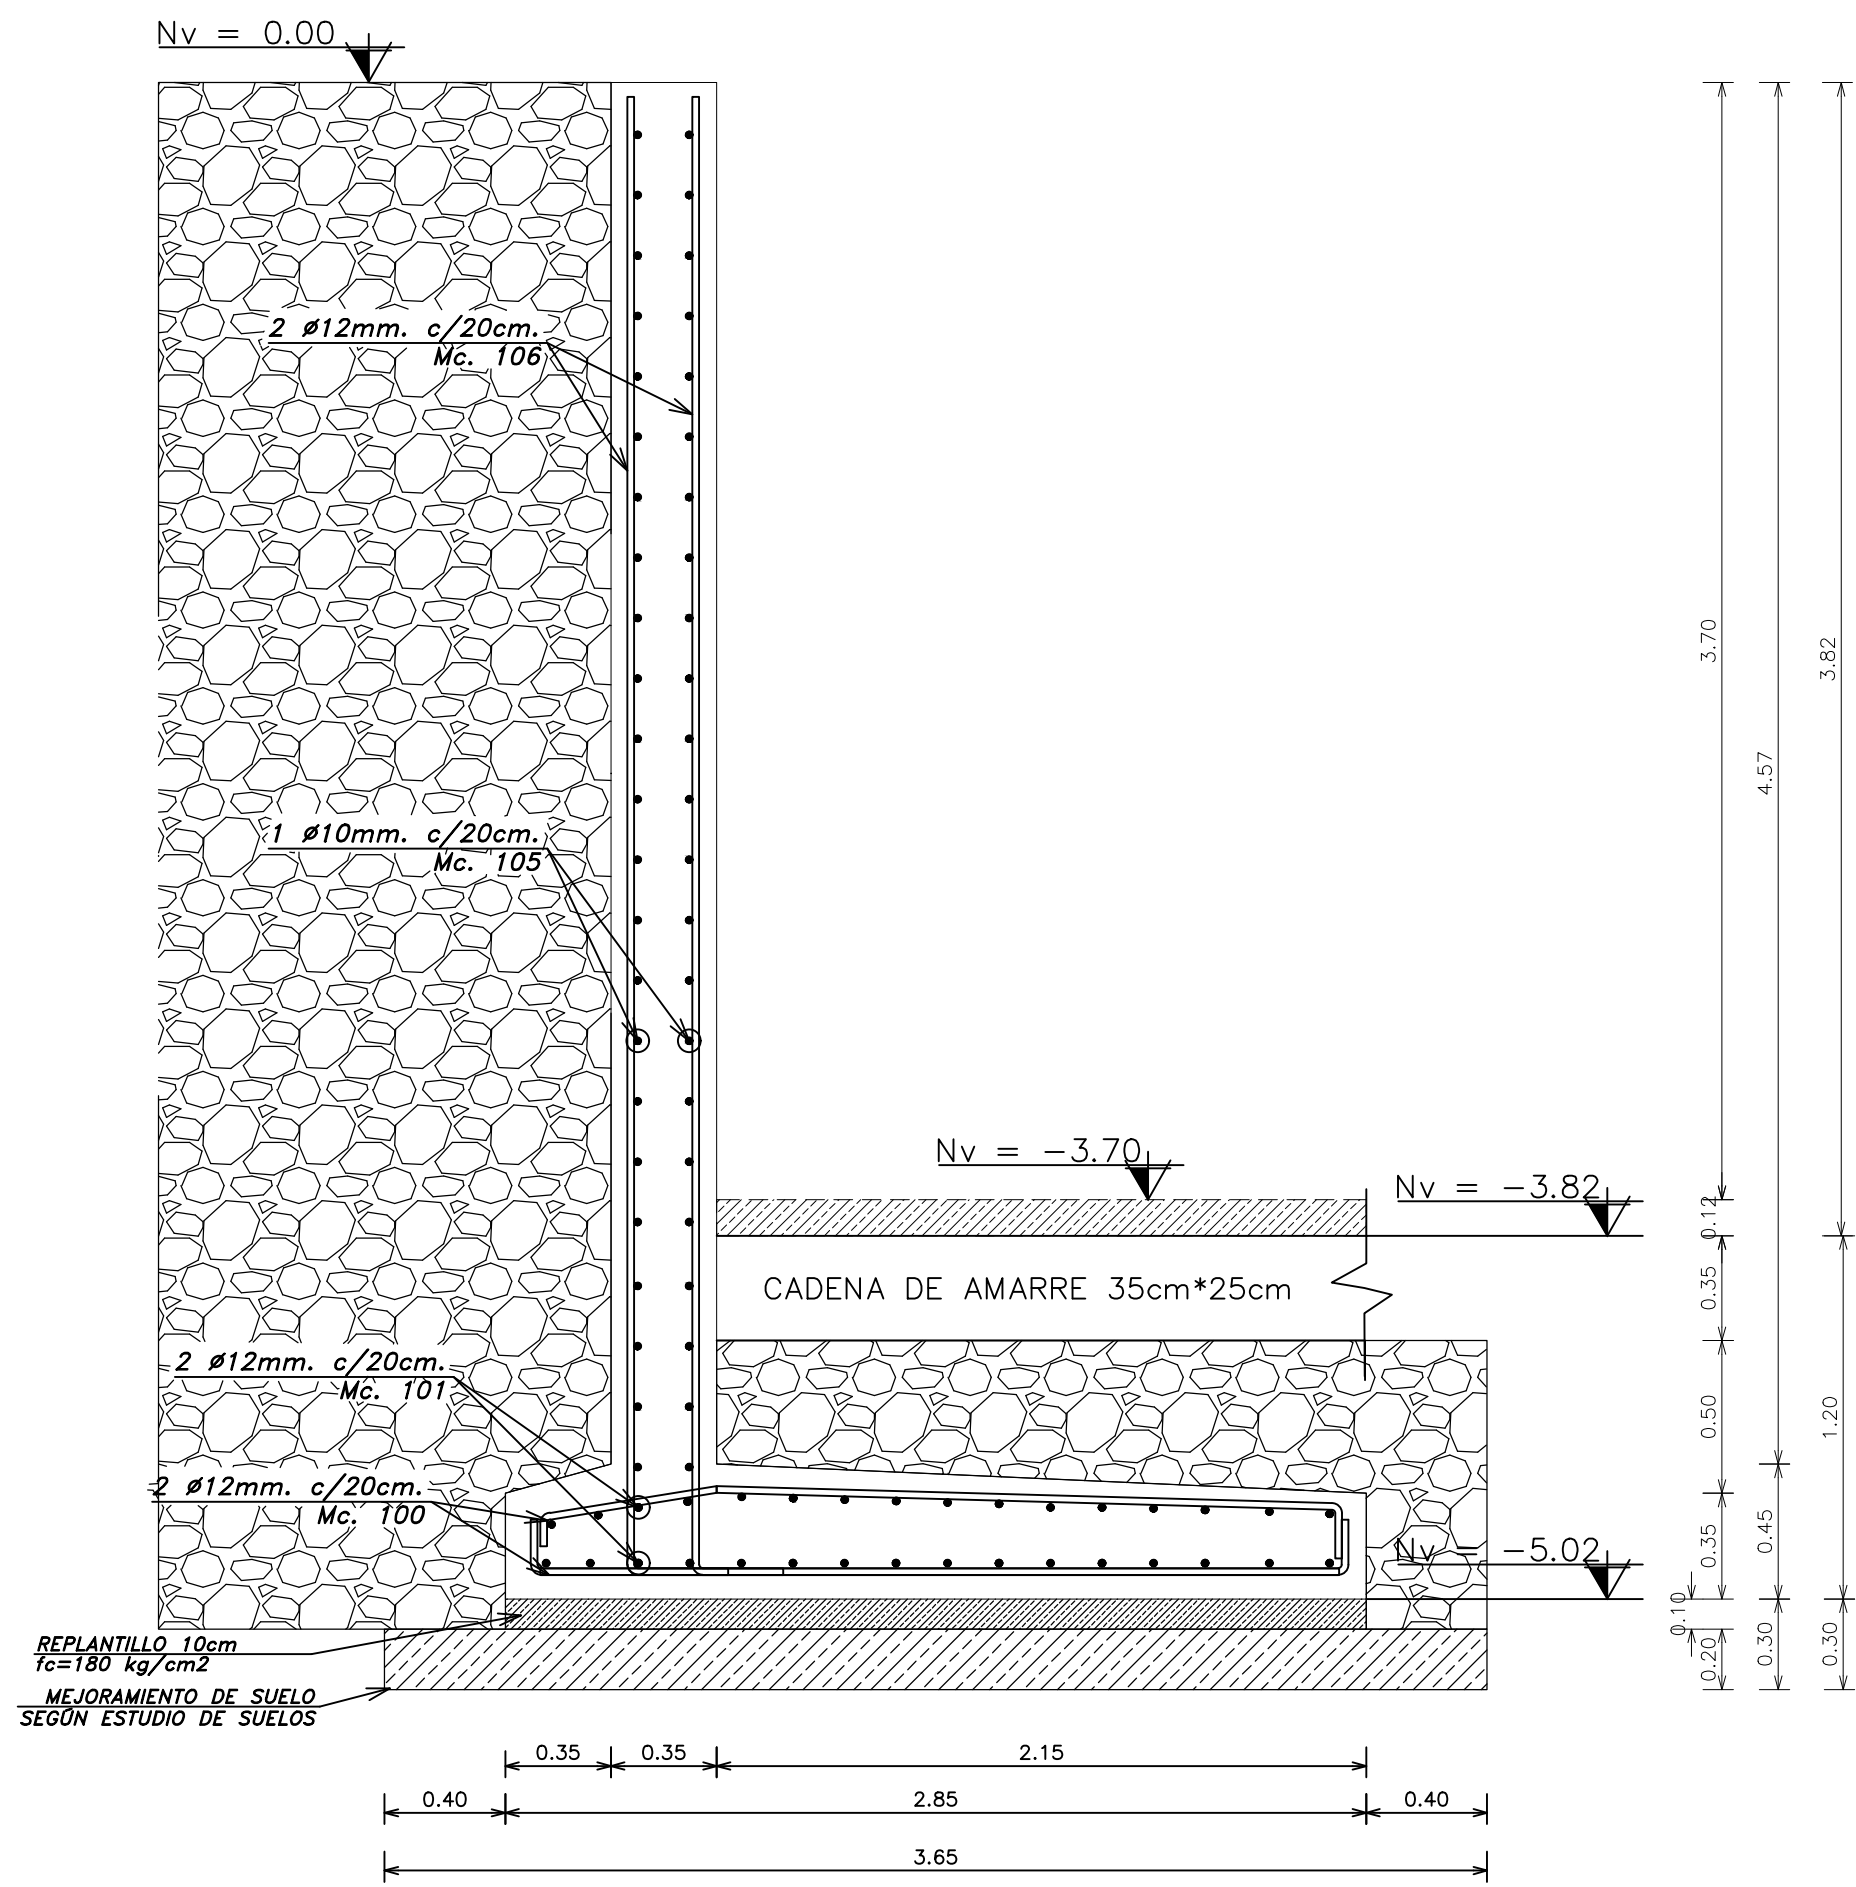


DETALLE DE MURO-ZAPATA CORRIDA P1
Escala 1:25

Especificaciones Técnicas de Cimentación

- 1.- RESISTENCIA CILINDRICA DEL HORMIGON SIMPLE $F_c=210 \text{ Kg/cm}^2$.
- 2.- LIMITE DE FLEUENCIA HIERRO REDONDO CORRUGADO $F_y=4200 \text{ Kg/cm}^2$.
- 3.- LONGITUD MINIMA DE TRASLAPE 40 DIAMETROS DE LA VARILLA.
- 4.- RECUBRIMIENTOS MINIMOS: CIMENTACION Y MUROS (3-5-7)cm. COLUMNAS Y VIGAS 3cm. CADENAS 2.5cm.
- 5.- TAMAÑO MAXIMO DEL AGREGADO GRUESO 3/4"
- 6.- RESISTENCIA ADMISIBLE DEL SUELO: SEGUN ESTUDIO 5 T/m2.
- 7.- REPLANTILLO $F_c=180 \text{ Kg/cm}^2$.
- 8.- PLACAS DE APOYO GRADO ASTM 572 A-50 ksi.

Tipos de Hierro Corrugado

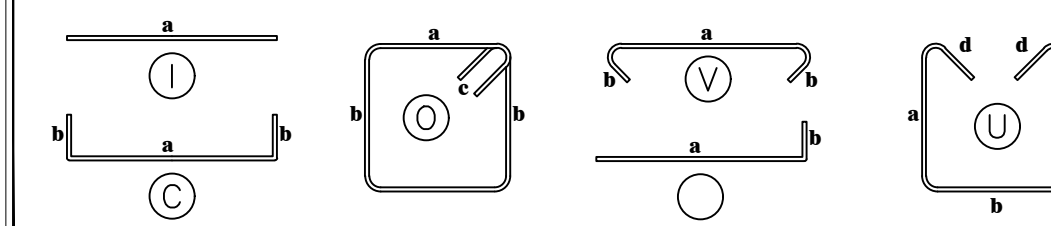

PROYECTO
BODEGAS FARINANGO

REPRESENTANTE LEGAL:

PROFESIONAL:

A.
CC.
PROPIETARIO:

ING. KARINA F. PANAMÁ QUIZHPI
REG. SENESCYT: 1001-2022-2433832
CC: 1723966071

UBICACION:

FECHA: SEPTIEMBRE - 2026

PREDIO:

DISEÑO: ING. KARINA PANAMÁ

DIBUJO: ING. KARINA PANAMÁ

ESCALA: INDICADA

CONTIENE:

CIMENTACIÓN

LAMINA:

A-1

SELLOS MUNICIPALES