




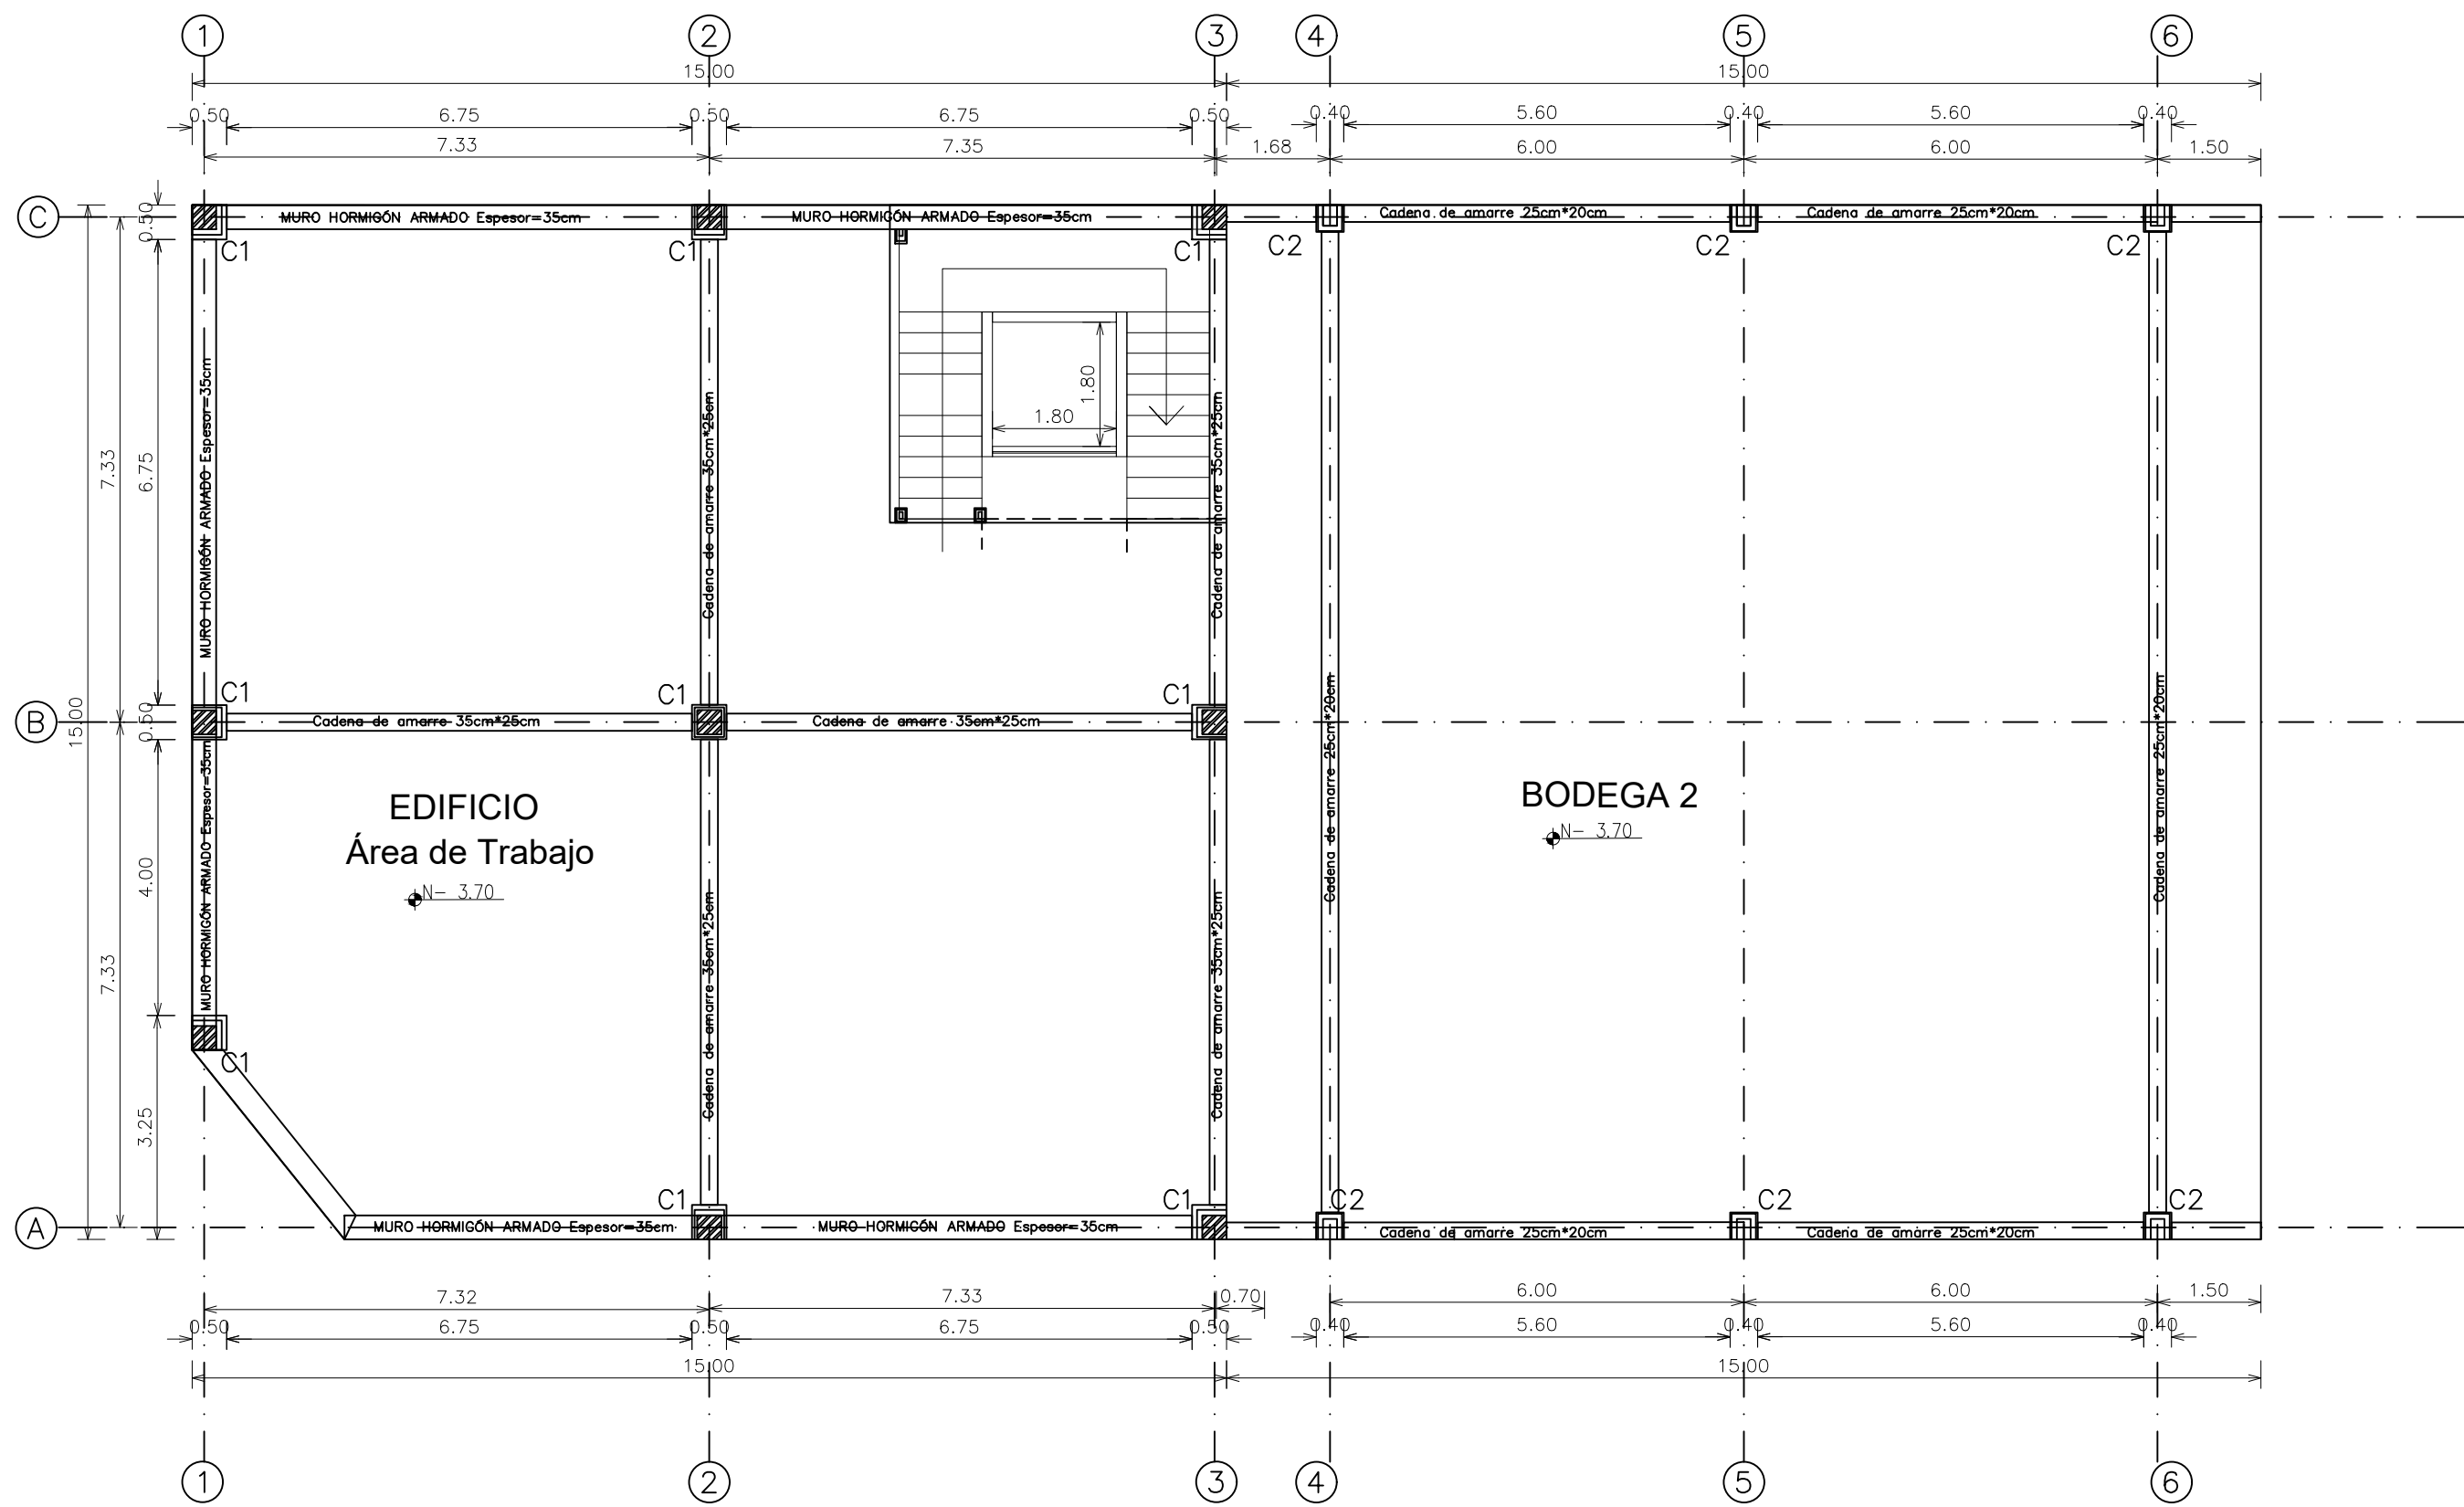


PLANTA COLUMNAS
Escala 1:100

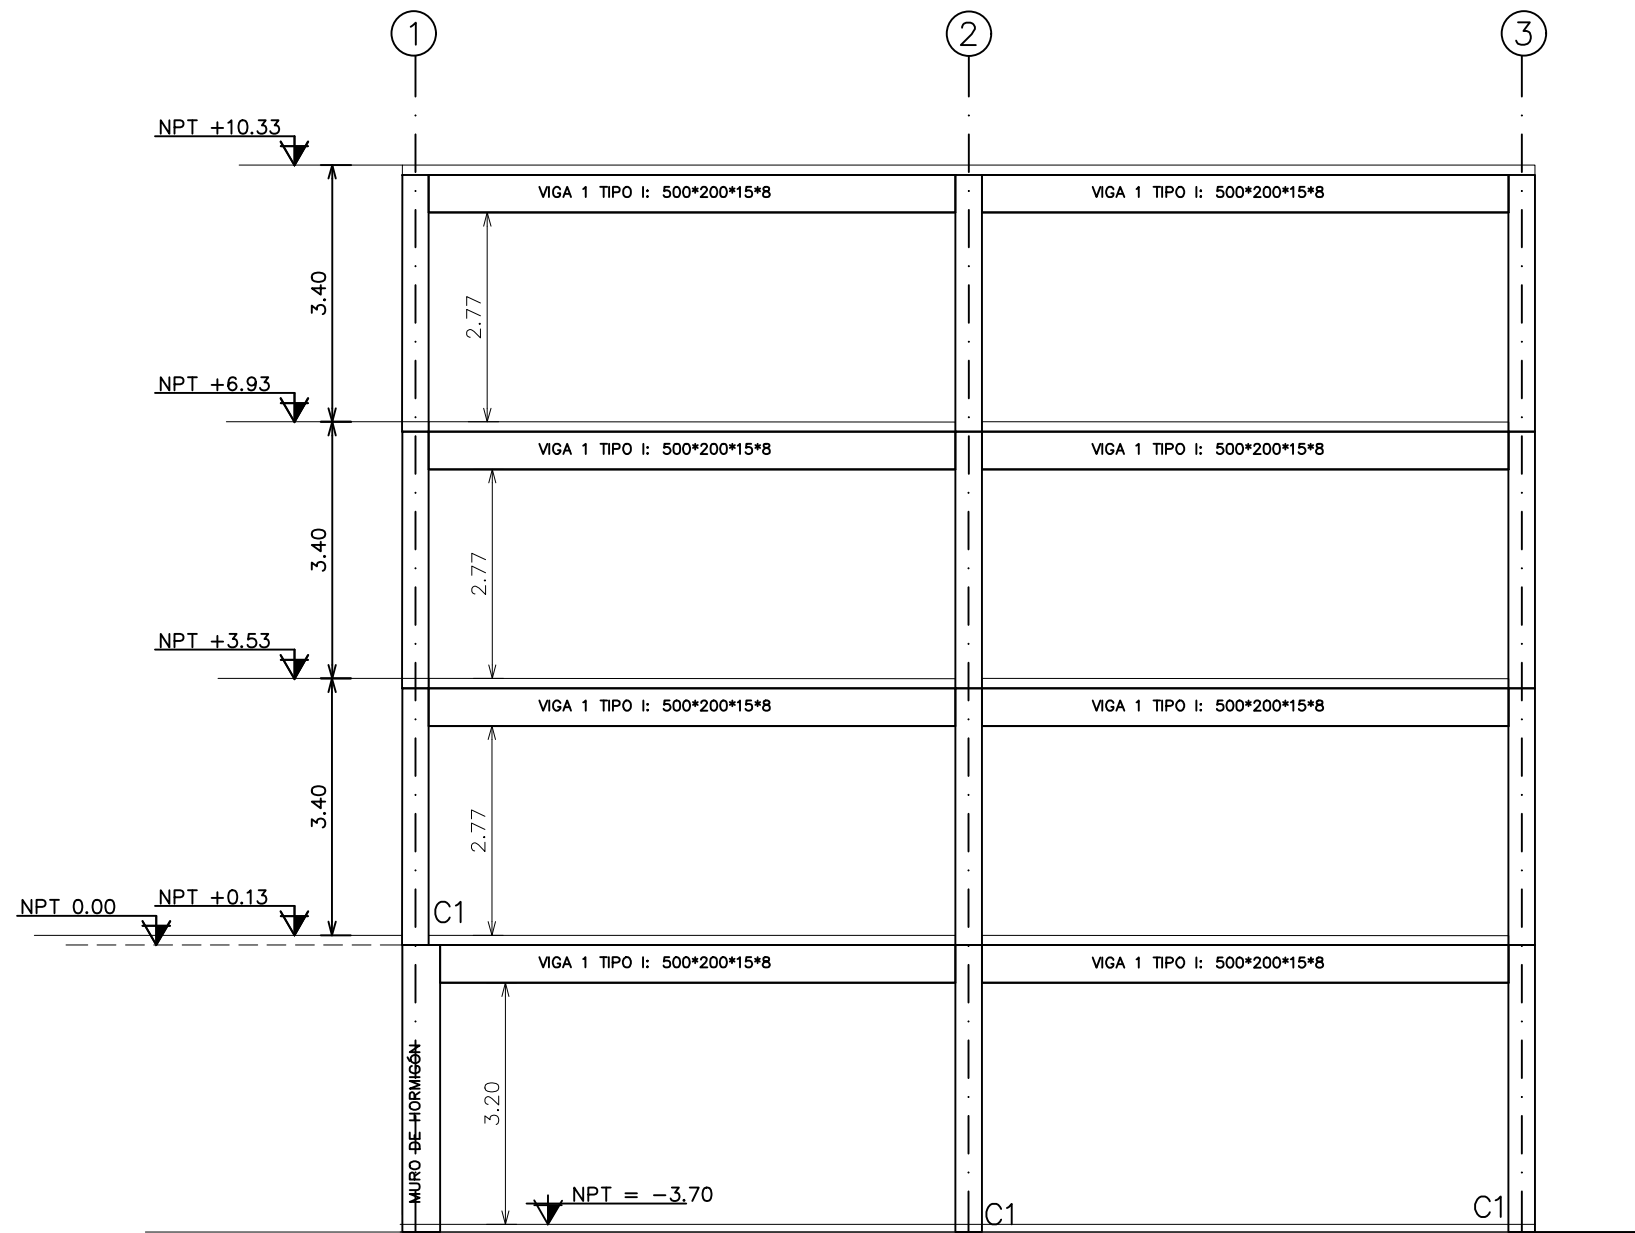


ELEVACIÓN EDIFICIO - EJE B
Escala 1:100

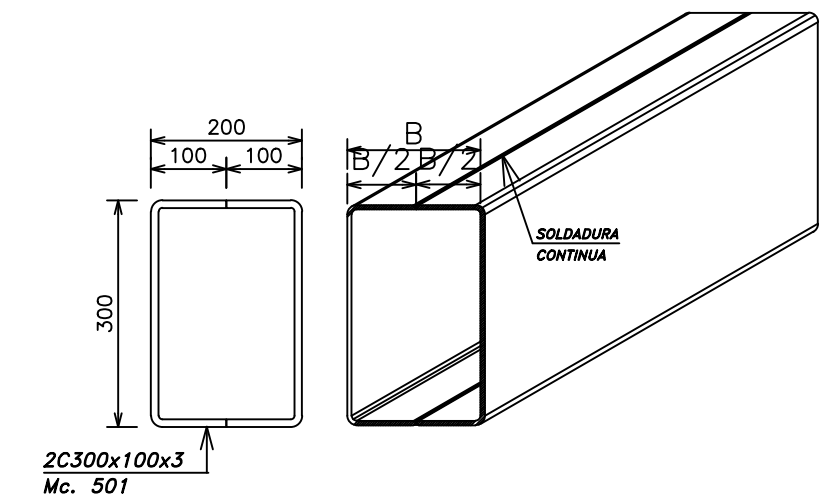


DETALLE COLUMNA C2
Escala 1:10

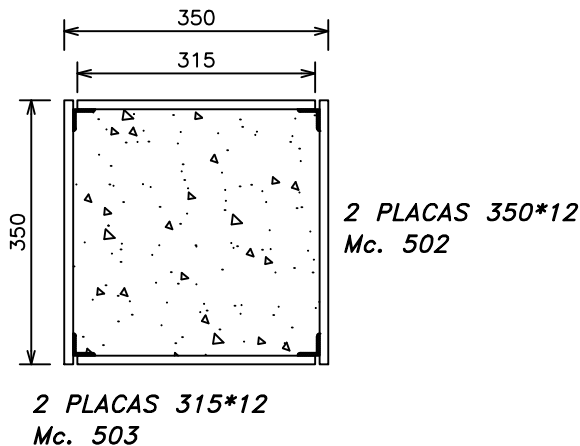


DETALLE COLUMNA C1
Escala 1:10

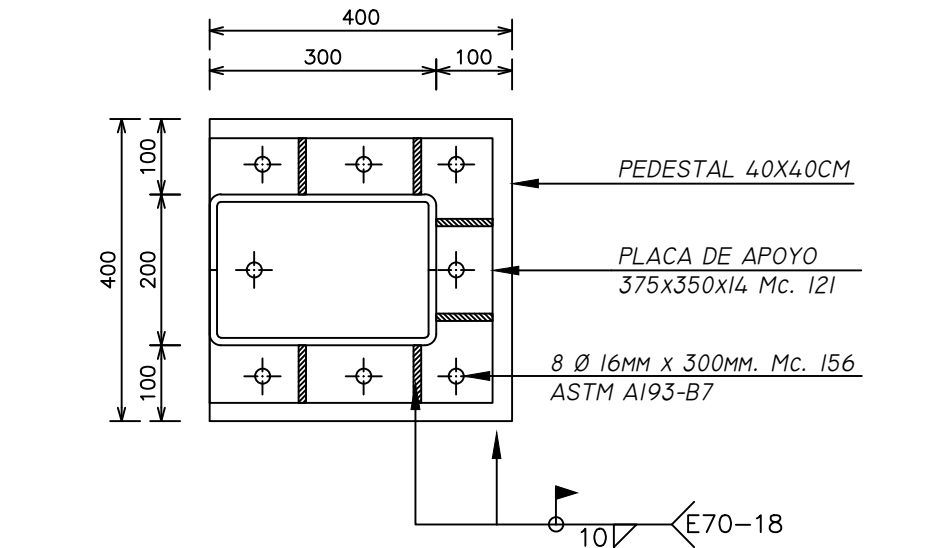


PLACA DE APOYO C2-(6u)
Escala 1:10

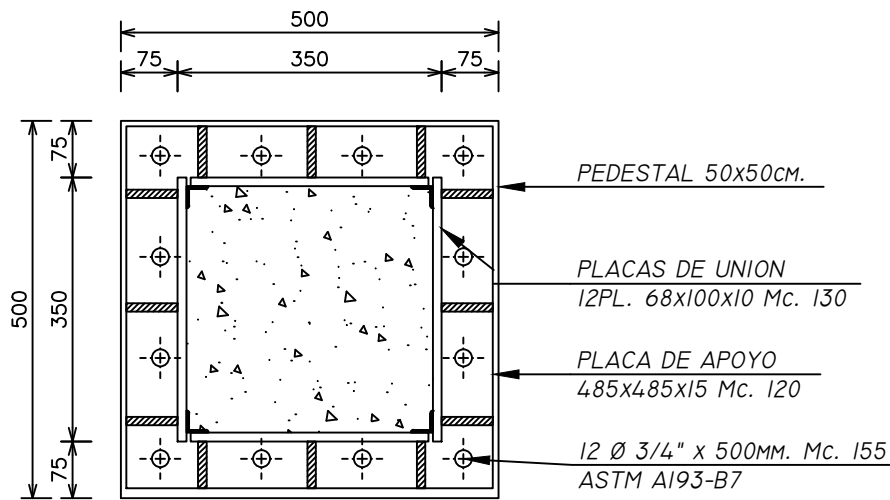


PLACA DE APOYO C1-CENTRAL
Escala 1:10

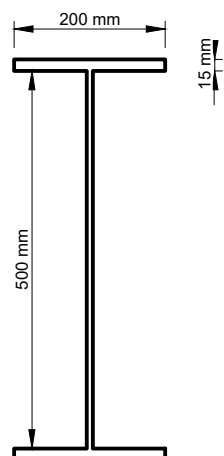


VIGA PRINCIPAL V1
Escala 1:10

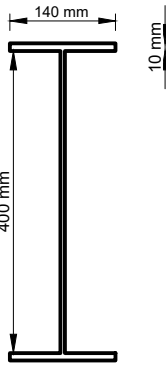


VIGA SECUNDARIA V2
Escala 1:10

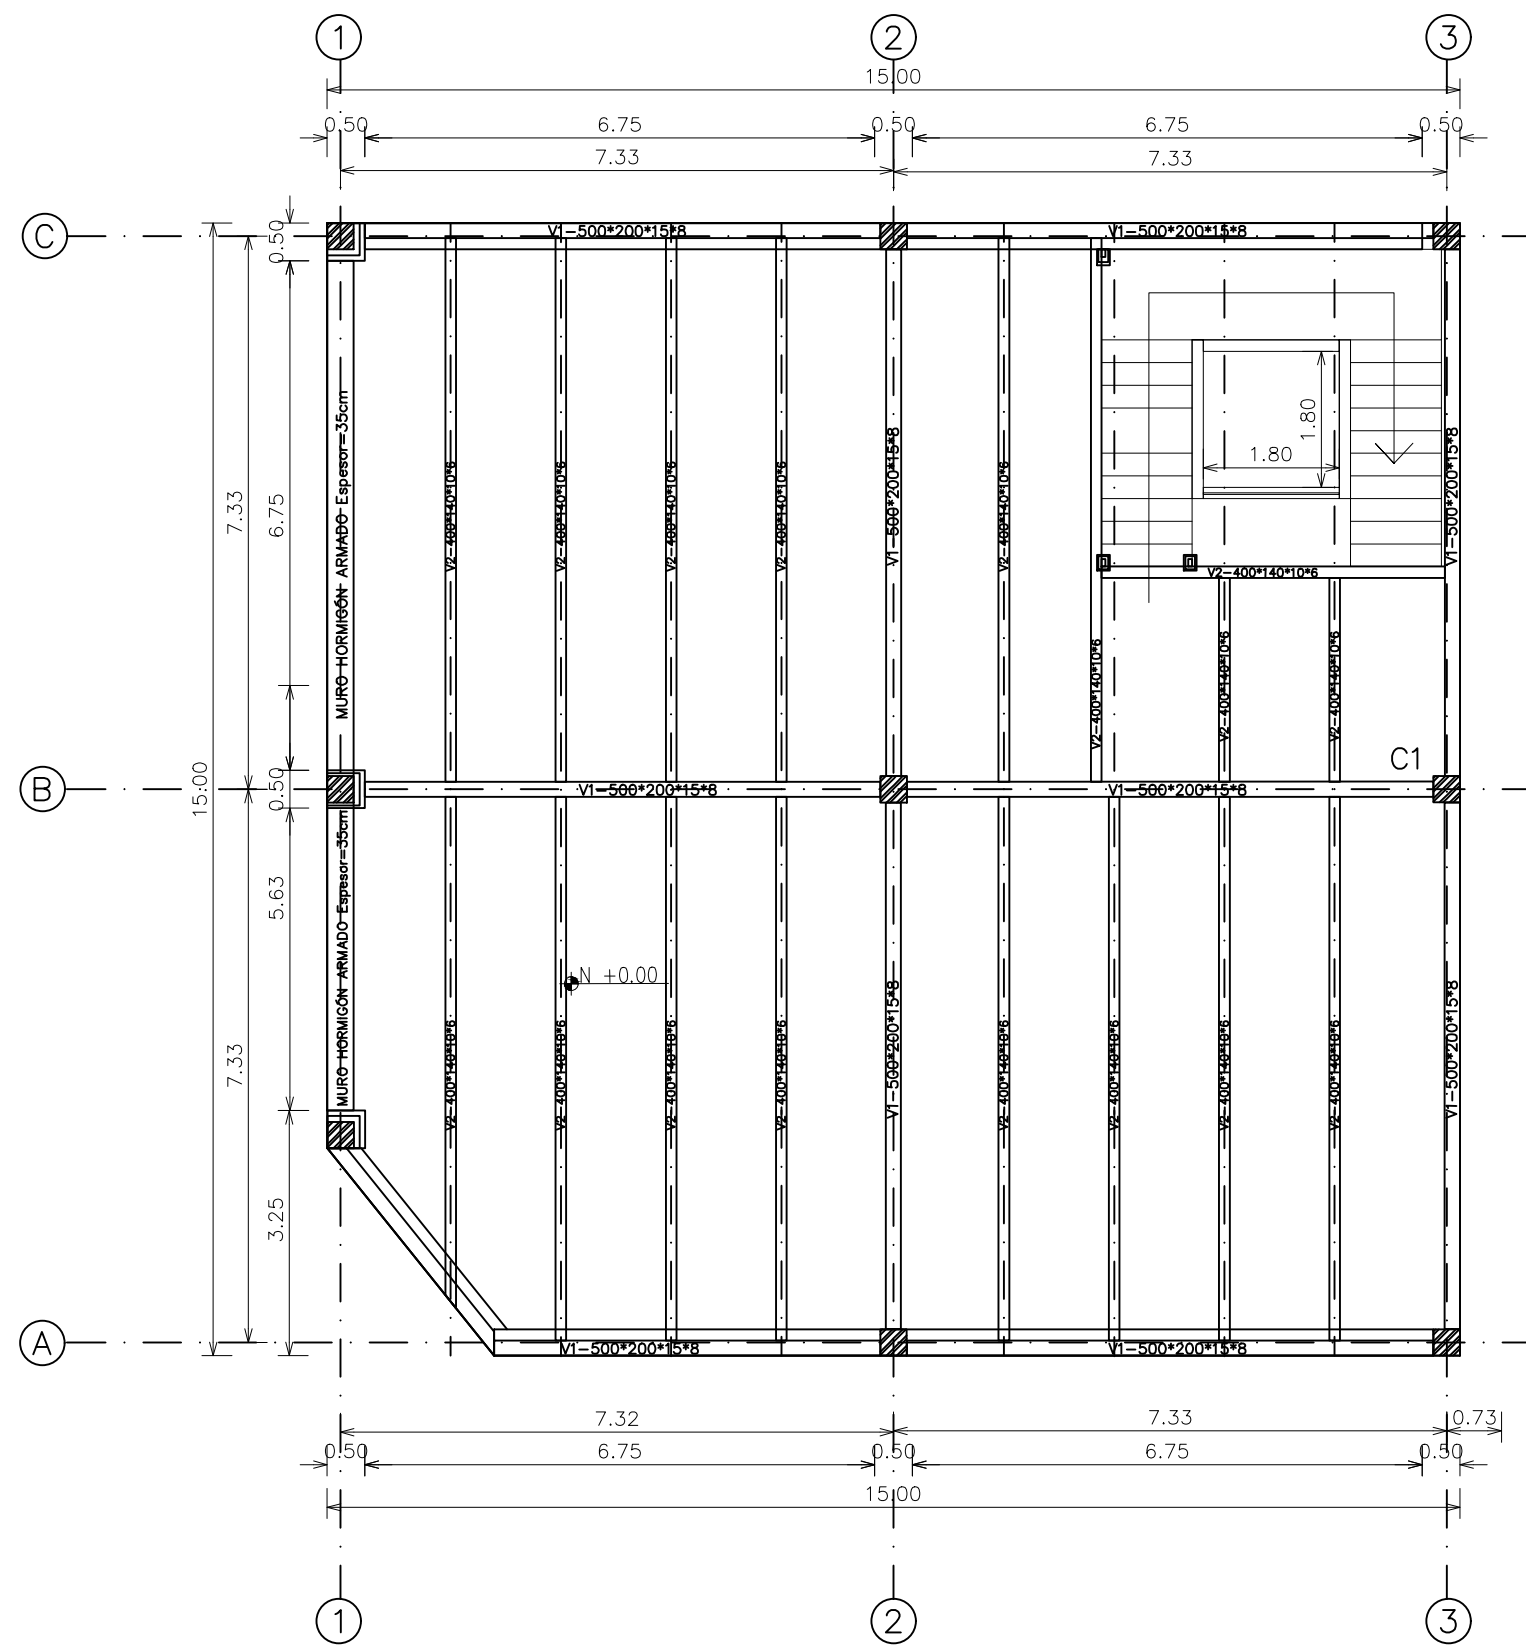

LOSA Nv.+0.13
Escala 1:100

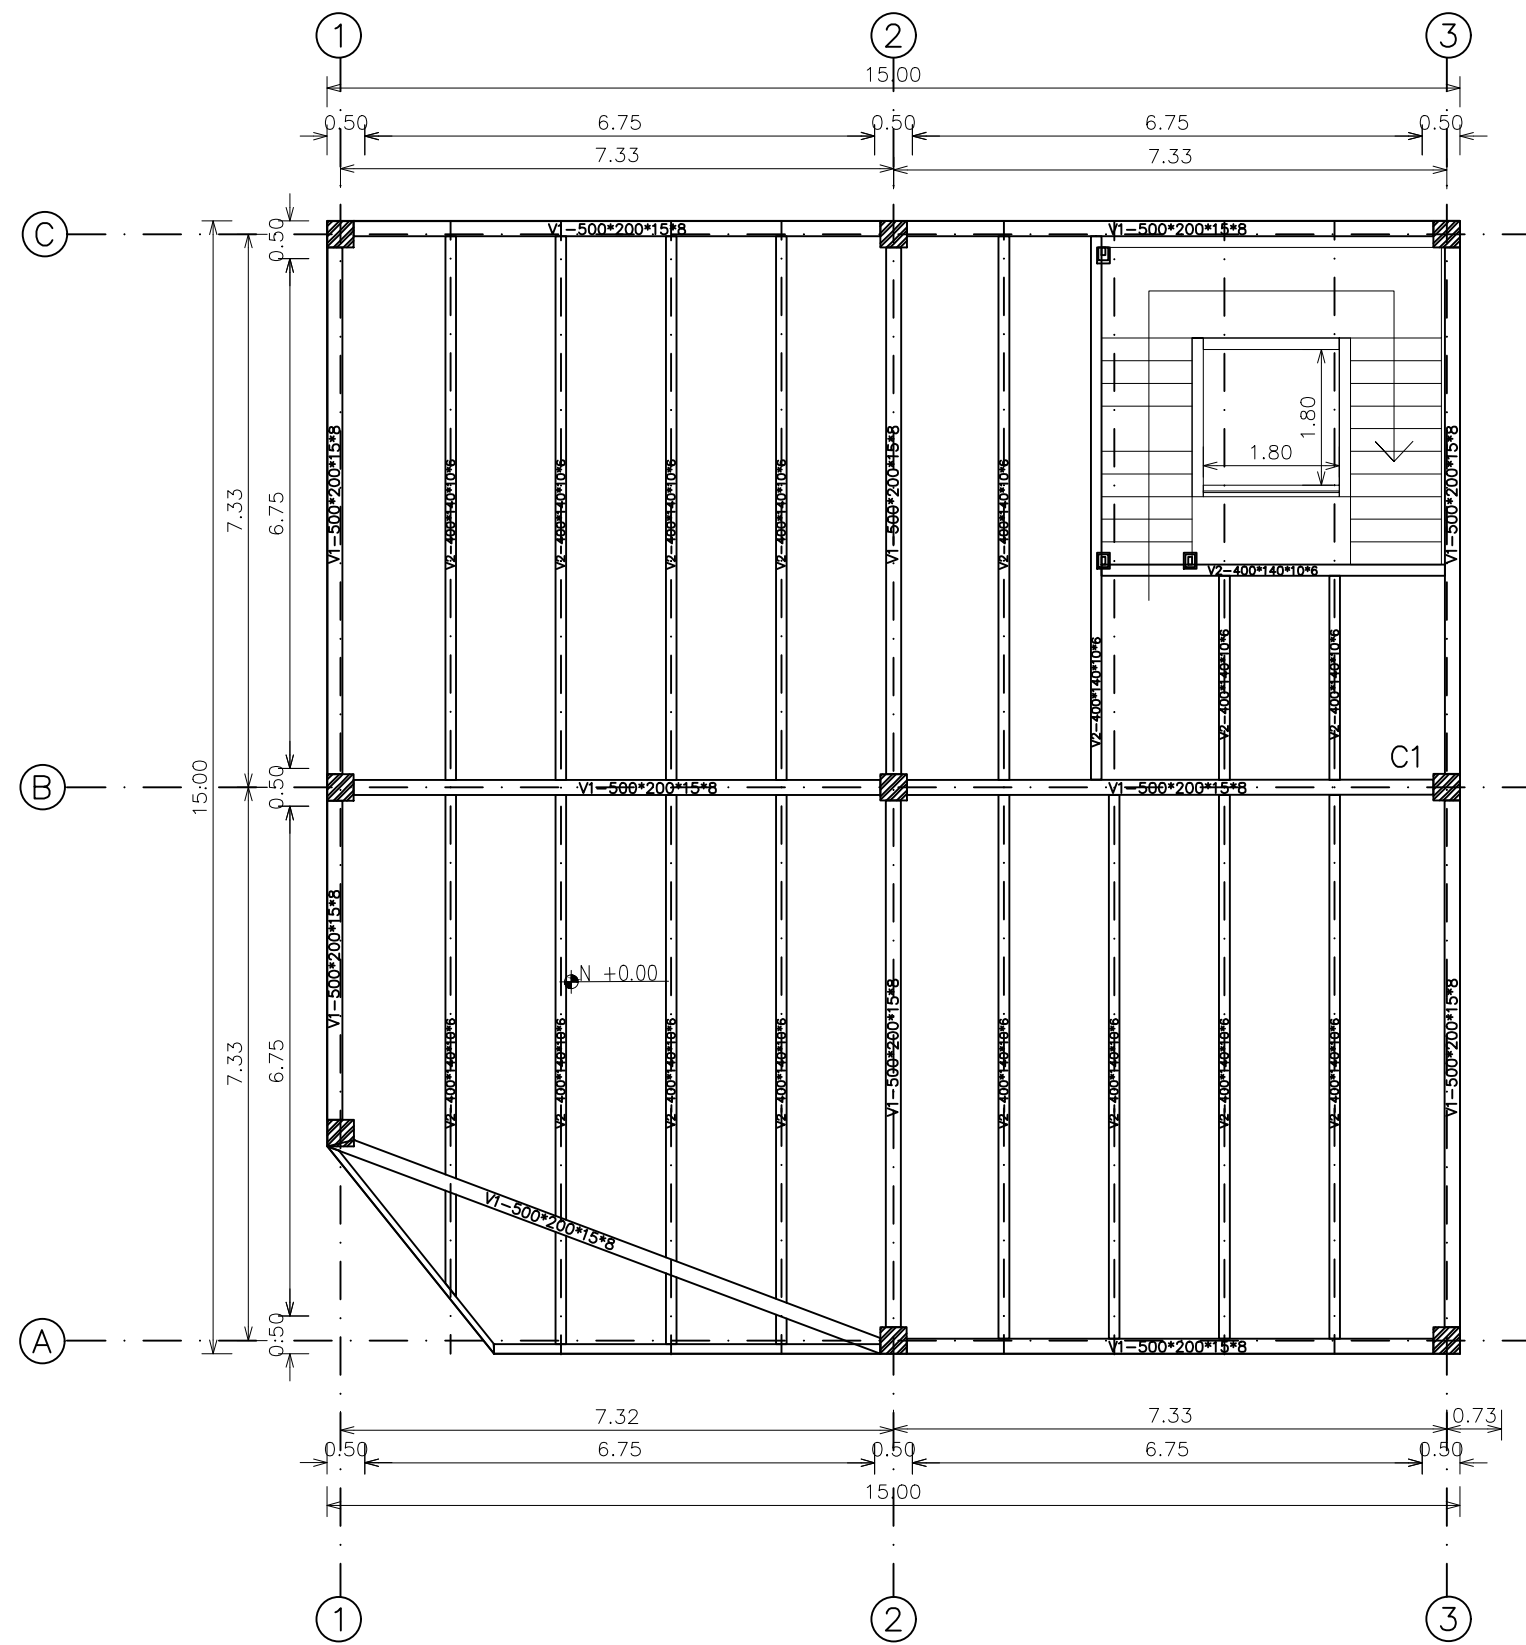

LOSA Nv.+3.53 Nv.+6.93 Nv.+10.33
Escala 1:100

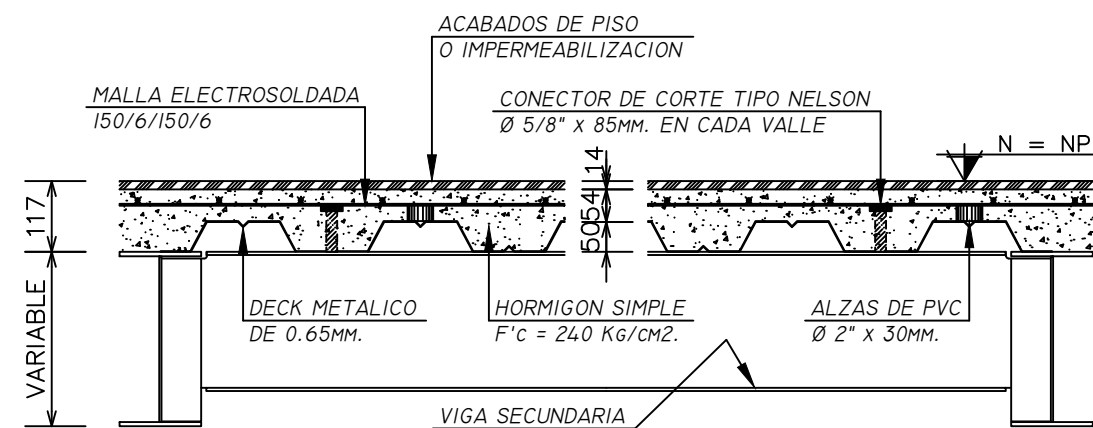


DETALLE SECCION TIPICA DE LOSETA
Escala S:N

Especificaciones Técnicas de Cimentación

- 1.- RESISTENCIA CILINDRICA DEL HORMIGON SIMPLE $F'c=210 \text{ Kg/cm}^2$.
- 2.- LIMITE DE FLEUENCIA HIERRO REDONDO CORRUGADO $Fy=4200 \text{ Kg/cm}^2$.
- 3.- LONGITUD MINIMA DE TRASLAPE 40 DIAMETROS DE LA VARILLA.
- 4.- RECUBRIMIENTOS MINIMOS: CIMENTACION Y MUROS (3-5-7)cm. COLUMNAS Y VIGAS 3cm. CADENAS 2.5cm.
- 5.- TAMAÑO MAXIMO DEL AGREGADO GRUESO 3/4"
- 6.- RESISTENCIA ADMISIBLE DEL SUELO: SEGUN ESTUDIO 5 T/m2.
- 7.- REPLANTILLO $F'c=180 \text{ Kg/cm}^2$.
- 8.- PLACAS DE APOYO GRADO ASTM 572 A-50 ksi.

Tipos de Hierro Corrugado

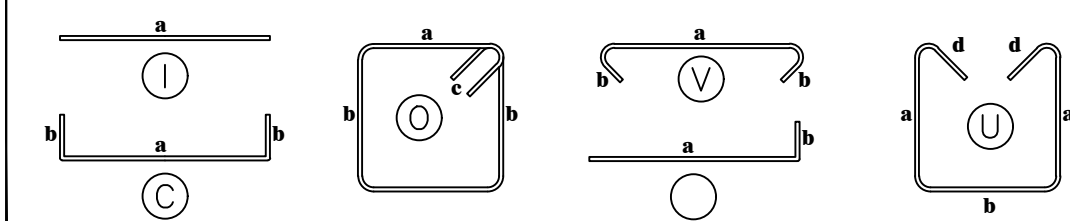

PROYECTO BODEGAS FARINANGO

REPRESENTANTE LEGAL:

A.
CC.
PROPIETARIO:

PROFESIONAL:

ING. KARINA F. PANAMÁ QUIZHPI
REG. SENESCYT: 1001-2022-2433832
CC: 1723966071

UBICACION:

PREDIO:

FECHA: SEPTIEMBRE - 2026

DISEÑO: ING. KARINA PANAMÁ
DIBUJO: ING. KARINA PANAMÁ

ESCALA: INDICADA

CONTIENE:

ESTRUCTURA-LOSAS DE EDIFICIO

LAMINA:

A-2

SELLOS MUNICIPALES