

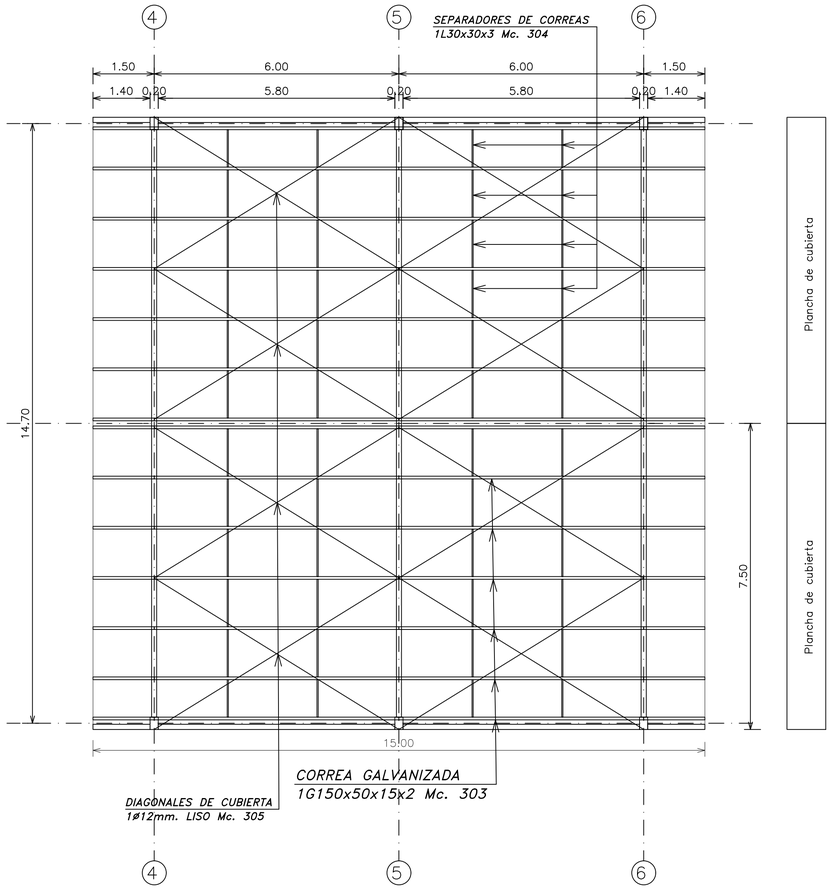


CUBIERTA BODEGA 2
Escala 1:75

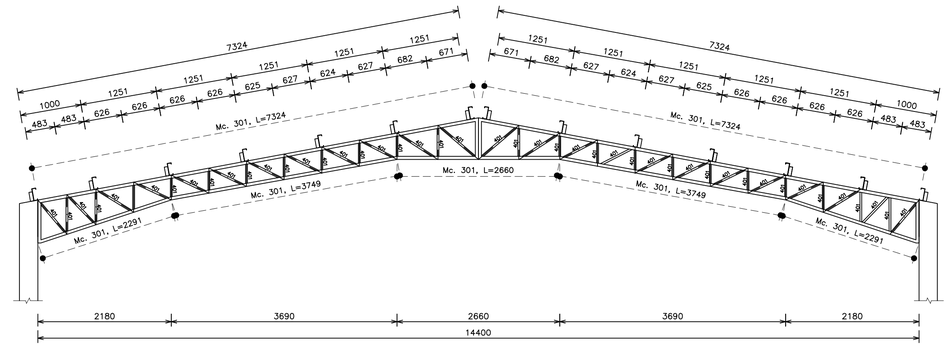

DETALLE DE VIGA TIPO 1
Escala 1:50

NOMENCLATURA		
Marca	Nro.	Perfiles
301	1	C 125 x 50 x 3
302	1	C 125 x 50 x 4
401	2	L 30 x 30 x 3
402	2	L 25 x 25 x 3

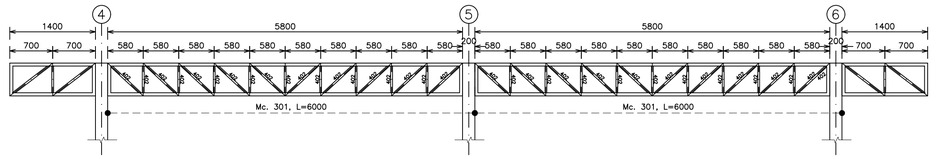


DETALLE DE VIGA TIPO 2
Escala 1:50

Especificaciones Técnicas de Cimentación

1.– RESISTENCIA CILINDRICA DEL HORMIGON SIMPLE F'c=210 Kg/cm2.
2.– LIMITE DE FLUENCIA HIERRO REDONDO CORRUGADO Fy=4200 Kg/cm2.
3.– LONGITUD MINIMA DE TRASLAPE 40 DIAMETROS DE LA VARILLA
4.– RECUBRIMIENTOS MINIMOS: CIMENTACION Y MUROS (3–5–7)cm. COLUMNAS Y VIGAS 3cm. CADENAS 2.5cm.
5.– TAMAÑO MAXIMO DEL AGREGADO GRUESO 3/4"
6.– RESISTENCIA ADMISIBLE DEL SUELO: SEGUN ESTUDIO 5 T/m2.
7.– REPLANTILLO F'c=180 Kg/cm2.
8.– PLACAS DE APOYO GRADO ASTM 572 A–50 ksi.

Tipos de Hierro Corrugado

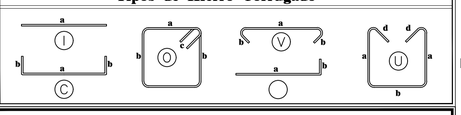

PROYECTO
BODEGAS FARINANGO

REPRESENTANTE LEGAL:

A
CC:
PROPIETARIO:

PROFESIONAL:

ING. KARINA F. PANAMÁ QUIZHPI
REG. SENESCYT: 1001-2022-2433832
CC: 1723966071

UBICACION:


PREDIO:

FECHA: SEPTIEMBRE-2026
DISEÑO: ING. KARINA PANAMÁ
DIBUJO: ING. KARINA PANAMÁ
ESCALA: INDICADA


CONTIENE:
BODEGA 2
DETALLE DE CUBIERTA, VIGAS Y CERCHAS

LAMINA:
A-3

SELLOS MUNICIPALES

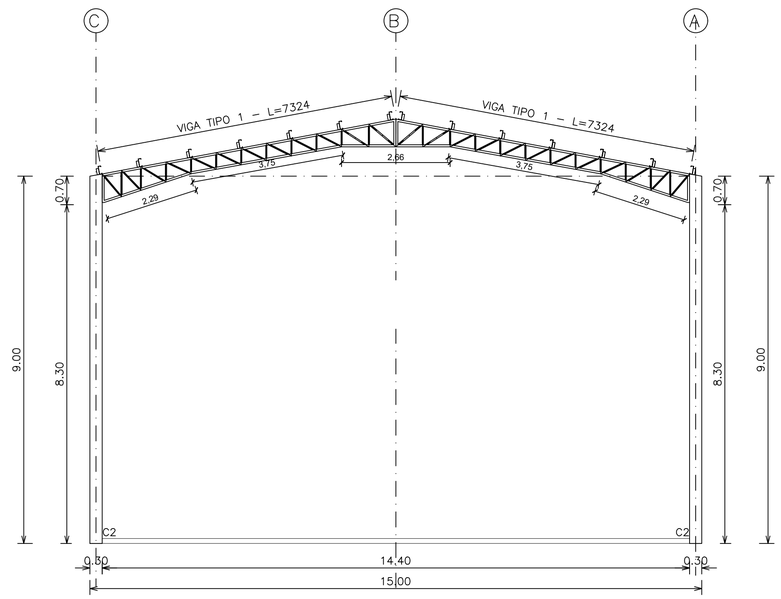

ELEVACIÓN PÓRTICO EJE 6 BODEGA 2.
Escala 1:75

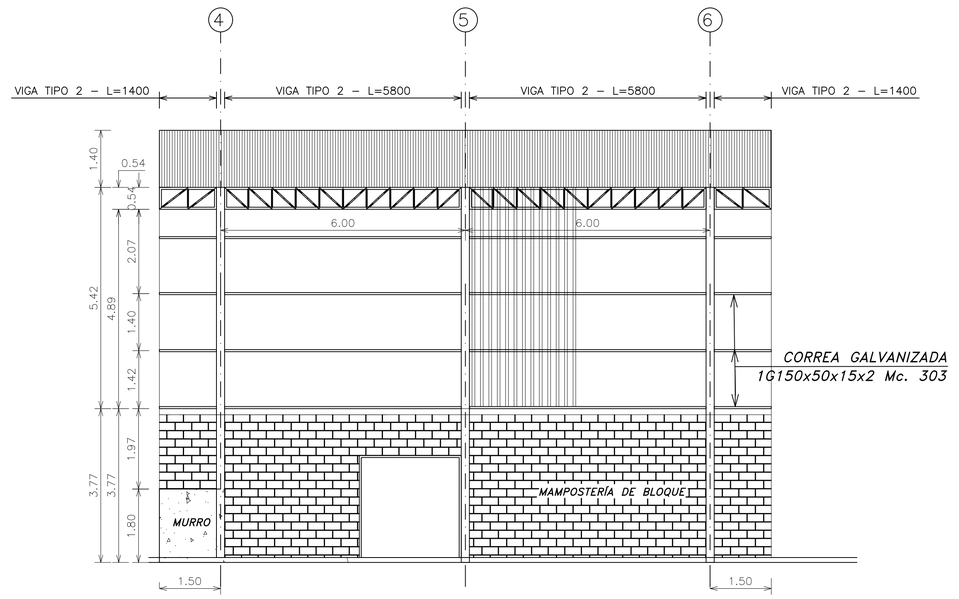

ELEVACIÓN PÓRTICO EJE A– BODEGA 2
Escala 1:100