
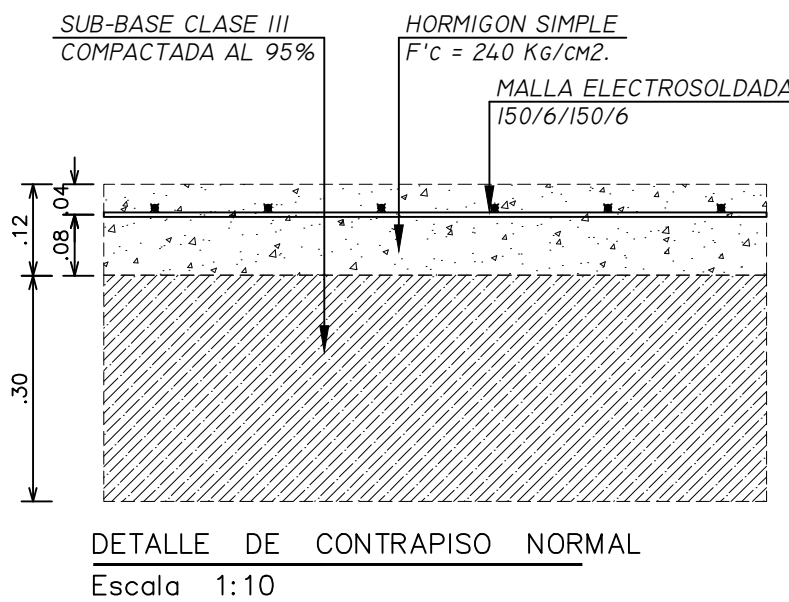
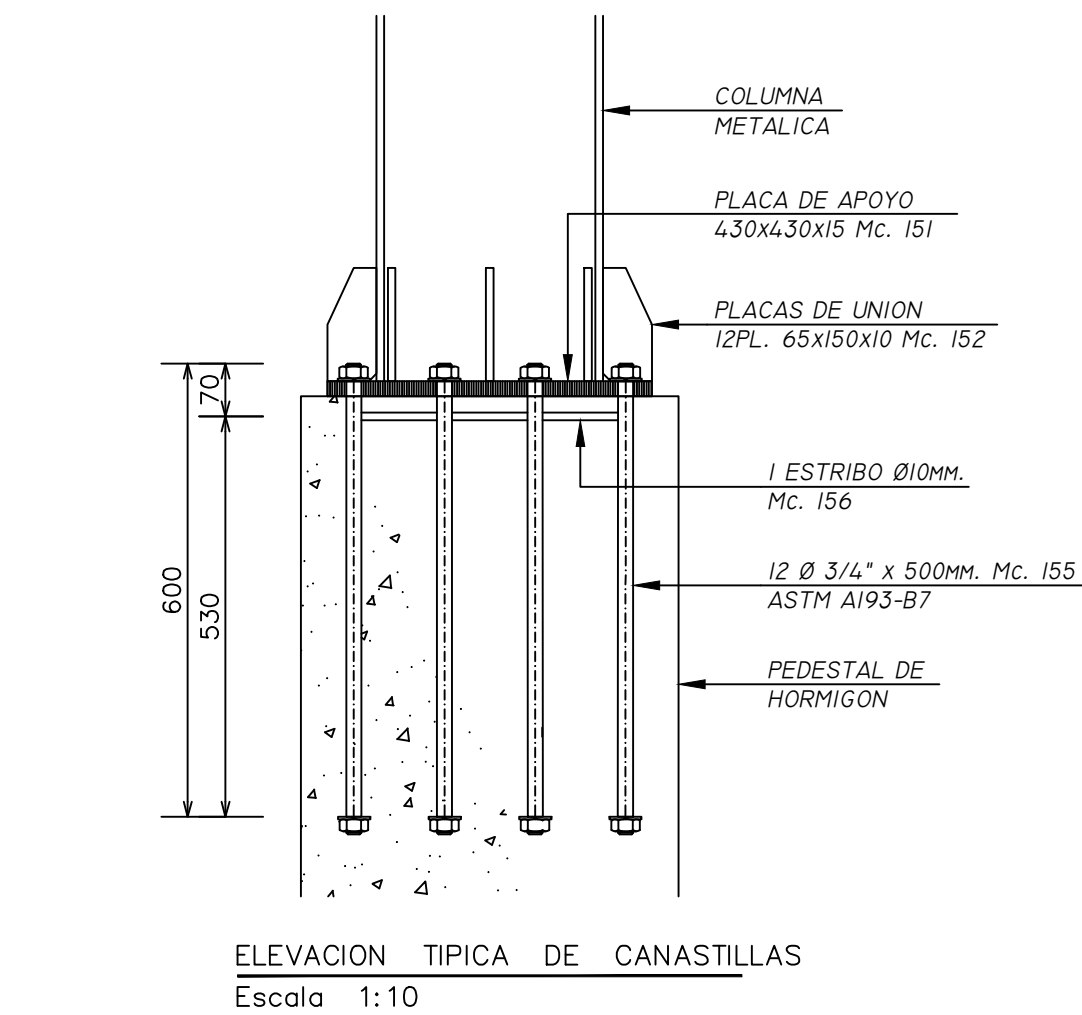
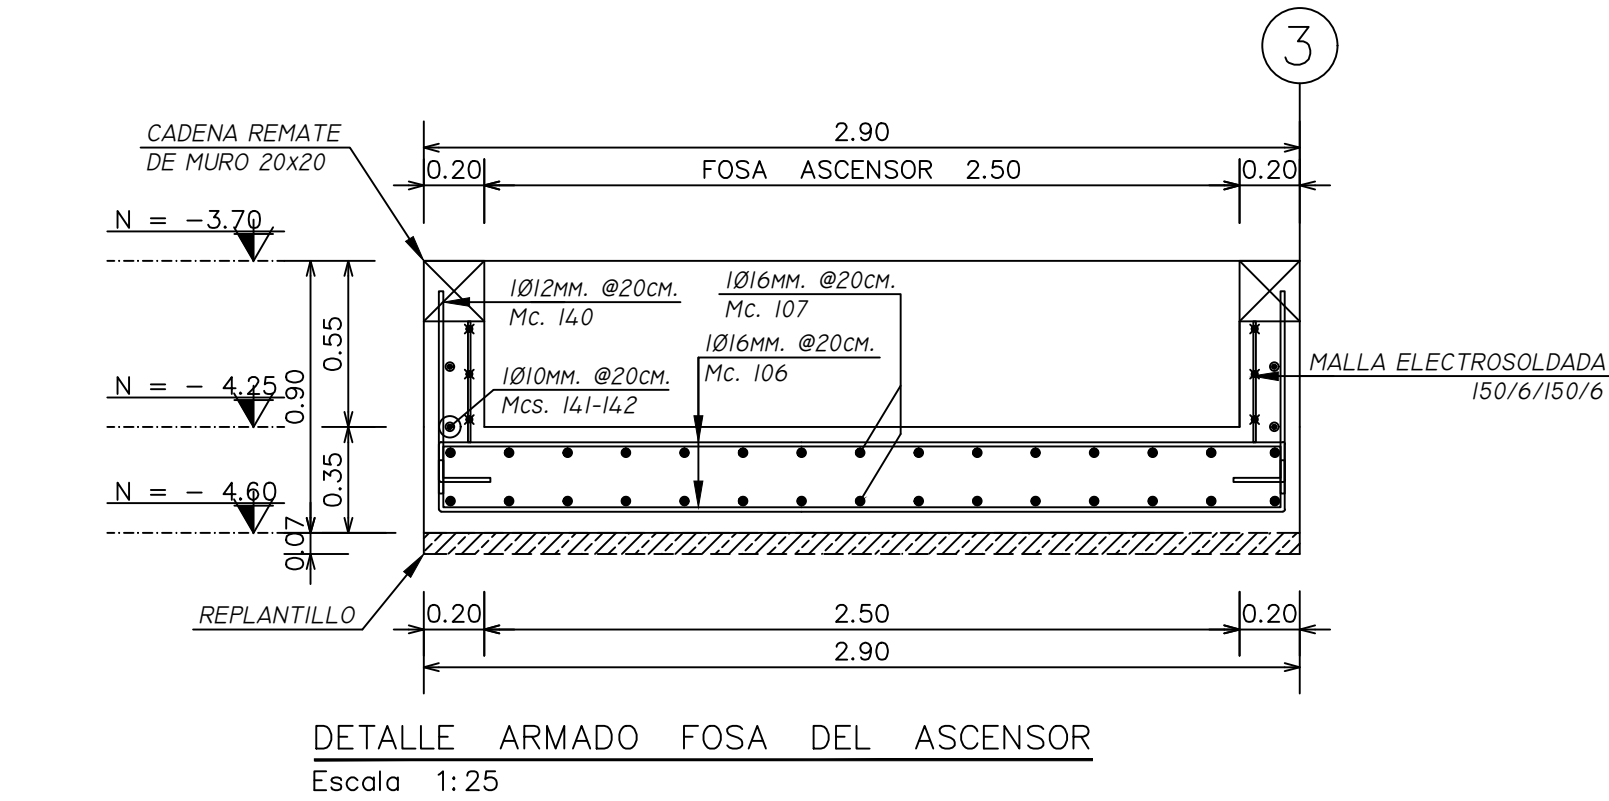
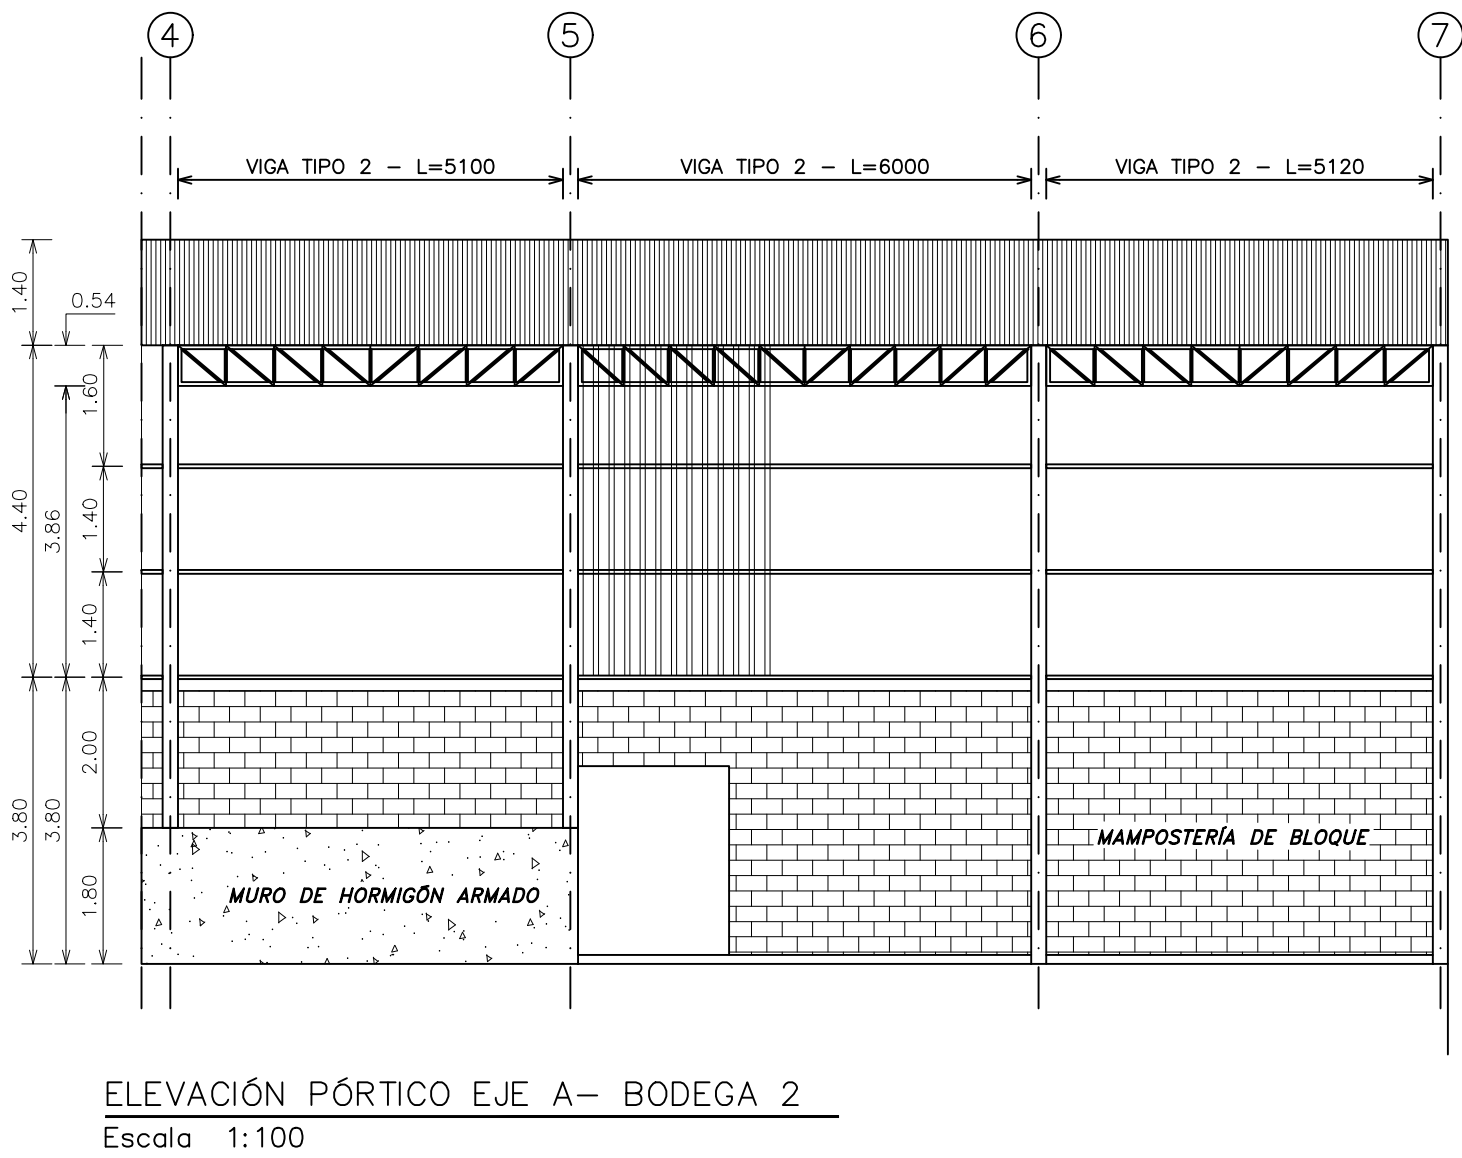
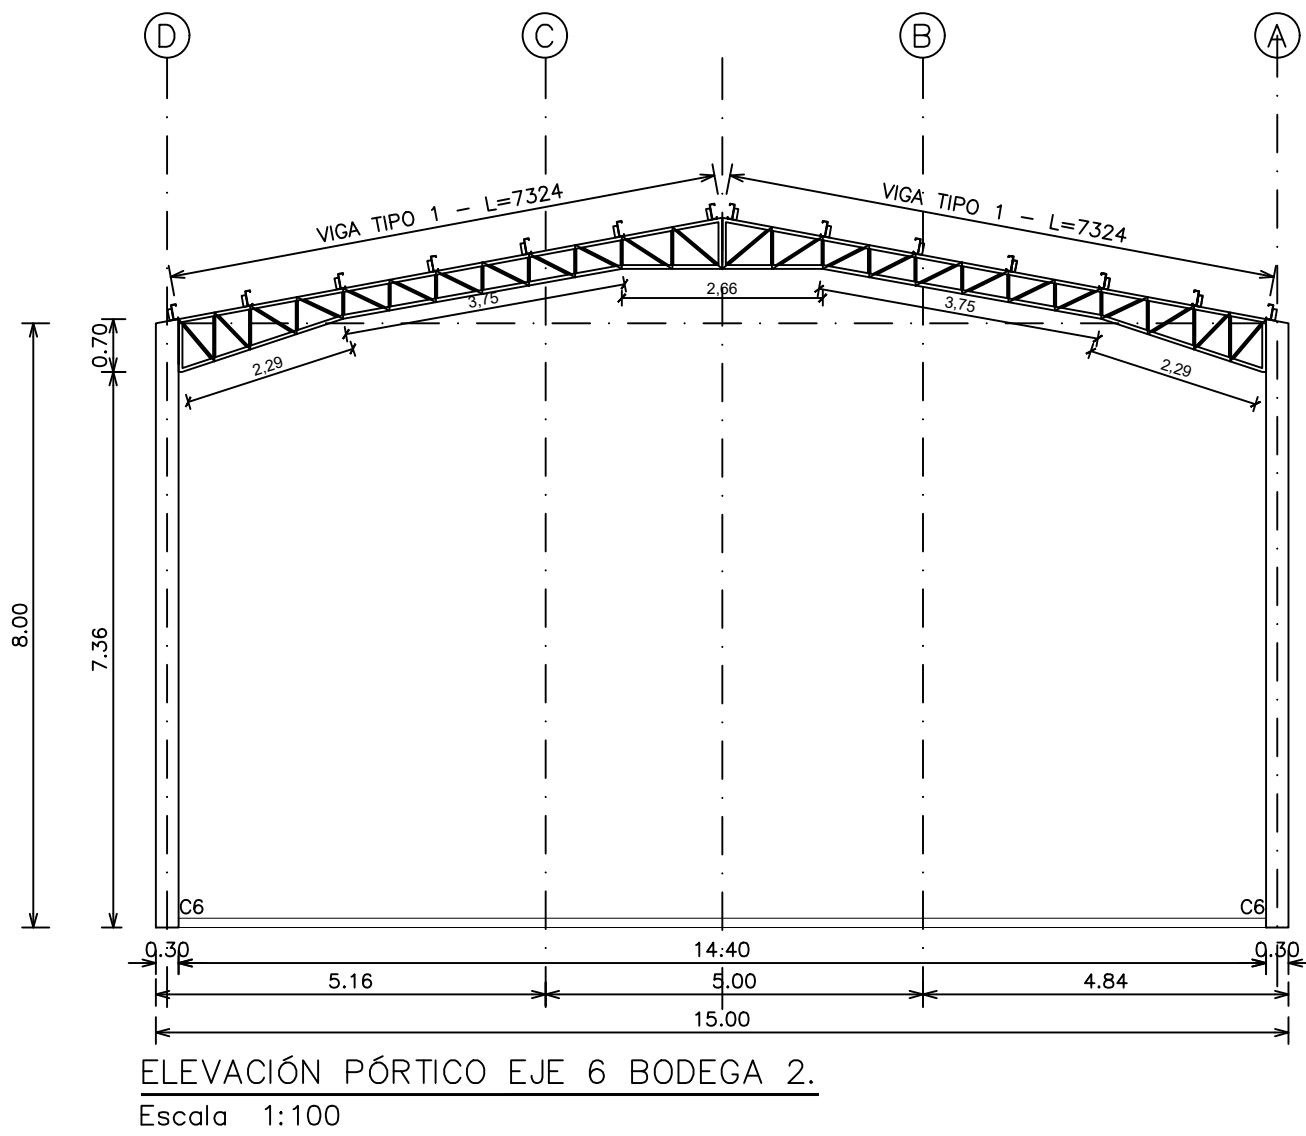


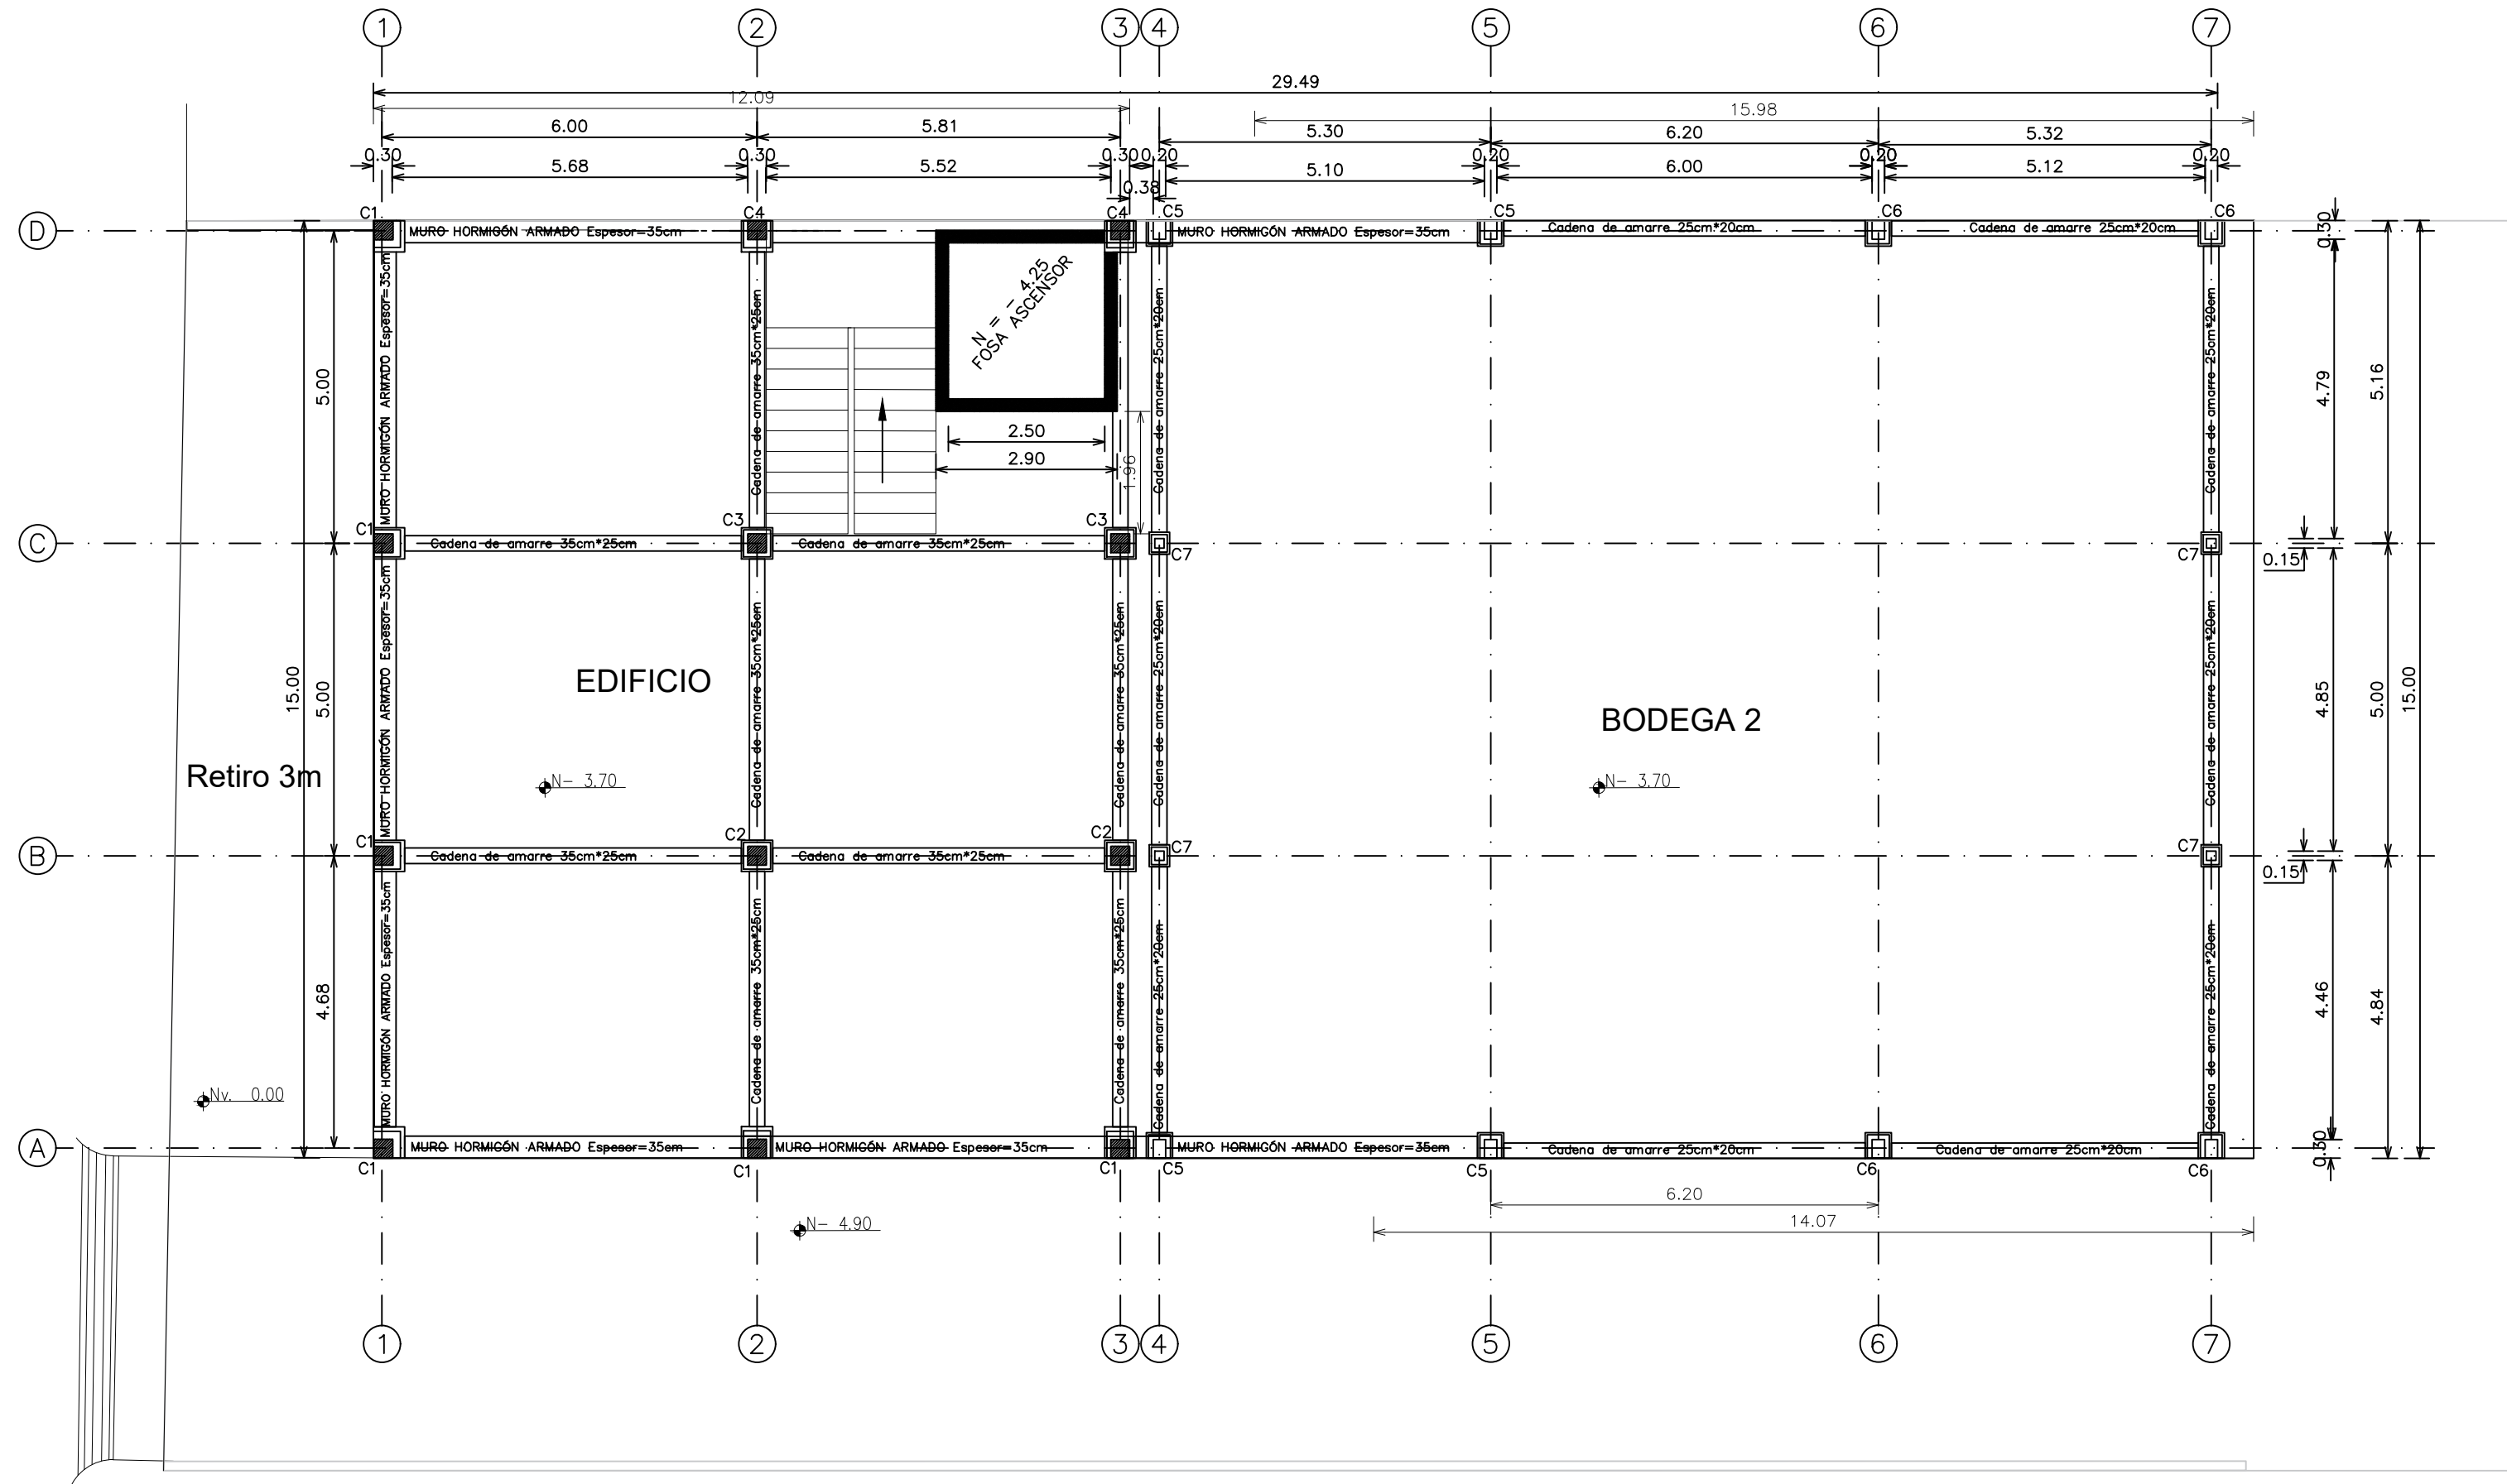

CUADRO DE COLUMNAS						
COLUMNAS C1	COLUMNAS C2	COLUMNAS C3	COLUMNAS C4	COLUMNAS C5	COLUMNAS C6	COLUMNAS C7
6u	2u	2u	2u	4u		

Especificaciones Técnicas de Cimentación

- RESISTENCIA CILINDRICA DEL HORMIGÓN SIMPLE $F'c=210 \text{ Kg/cm}^2$.
- LÍMITE DE FLEUENCIA HIERRO REDONDO CORRUGADO $f_y=4200 \text{ Kg/cm}^2$.
- LONGITUD MINIMA DE TRASLAPÉ 40 DIAMETROS DE LA VARILLA.
- RECUBRIMIENTOS MINIMOS: CIMENTACION Y MUROS (3-5-7)cm. COLUMNAS Y VIGAS 3cm. CADENAS 2.5cm.
- TAMARO MAXIMO DEL AGREGADO GRUESO 3/4"
- RESISTENCIA ADMISIBLE DEL SUELO: SEGUN ESTUDIO 5 T/m2.
- REPLANTILLO $F'c=180 \text{ Kg/cm}^2$.
- PLACAS DE APOYO GRADO ASTM 572 A-50 ksi.

Tipos de Hierro Corrugado

PROYECTO BODEGAS FARINANGO

REPRESENTANTE LEGAL:

A
CC:
PROPIETARIO:

PROFESIONAL:

ING. KARINA F. PANAMÁ QUIZHPI
REG. SENESCYT: 1001-2022-2433832
CC: 1723966071

UBICACION:

FECHA: JULIO-2026

PREDIO:

DISEÑO: ING. KARINA PANAMÁ
DIBUJO: ING. KARINA PANAMÁ
ESCALA: INDICADA

CONTIENE:
CIMENTACIÓN

LAMINA:
A-2

Sellos Municipales