



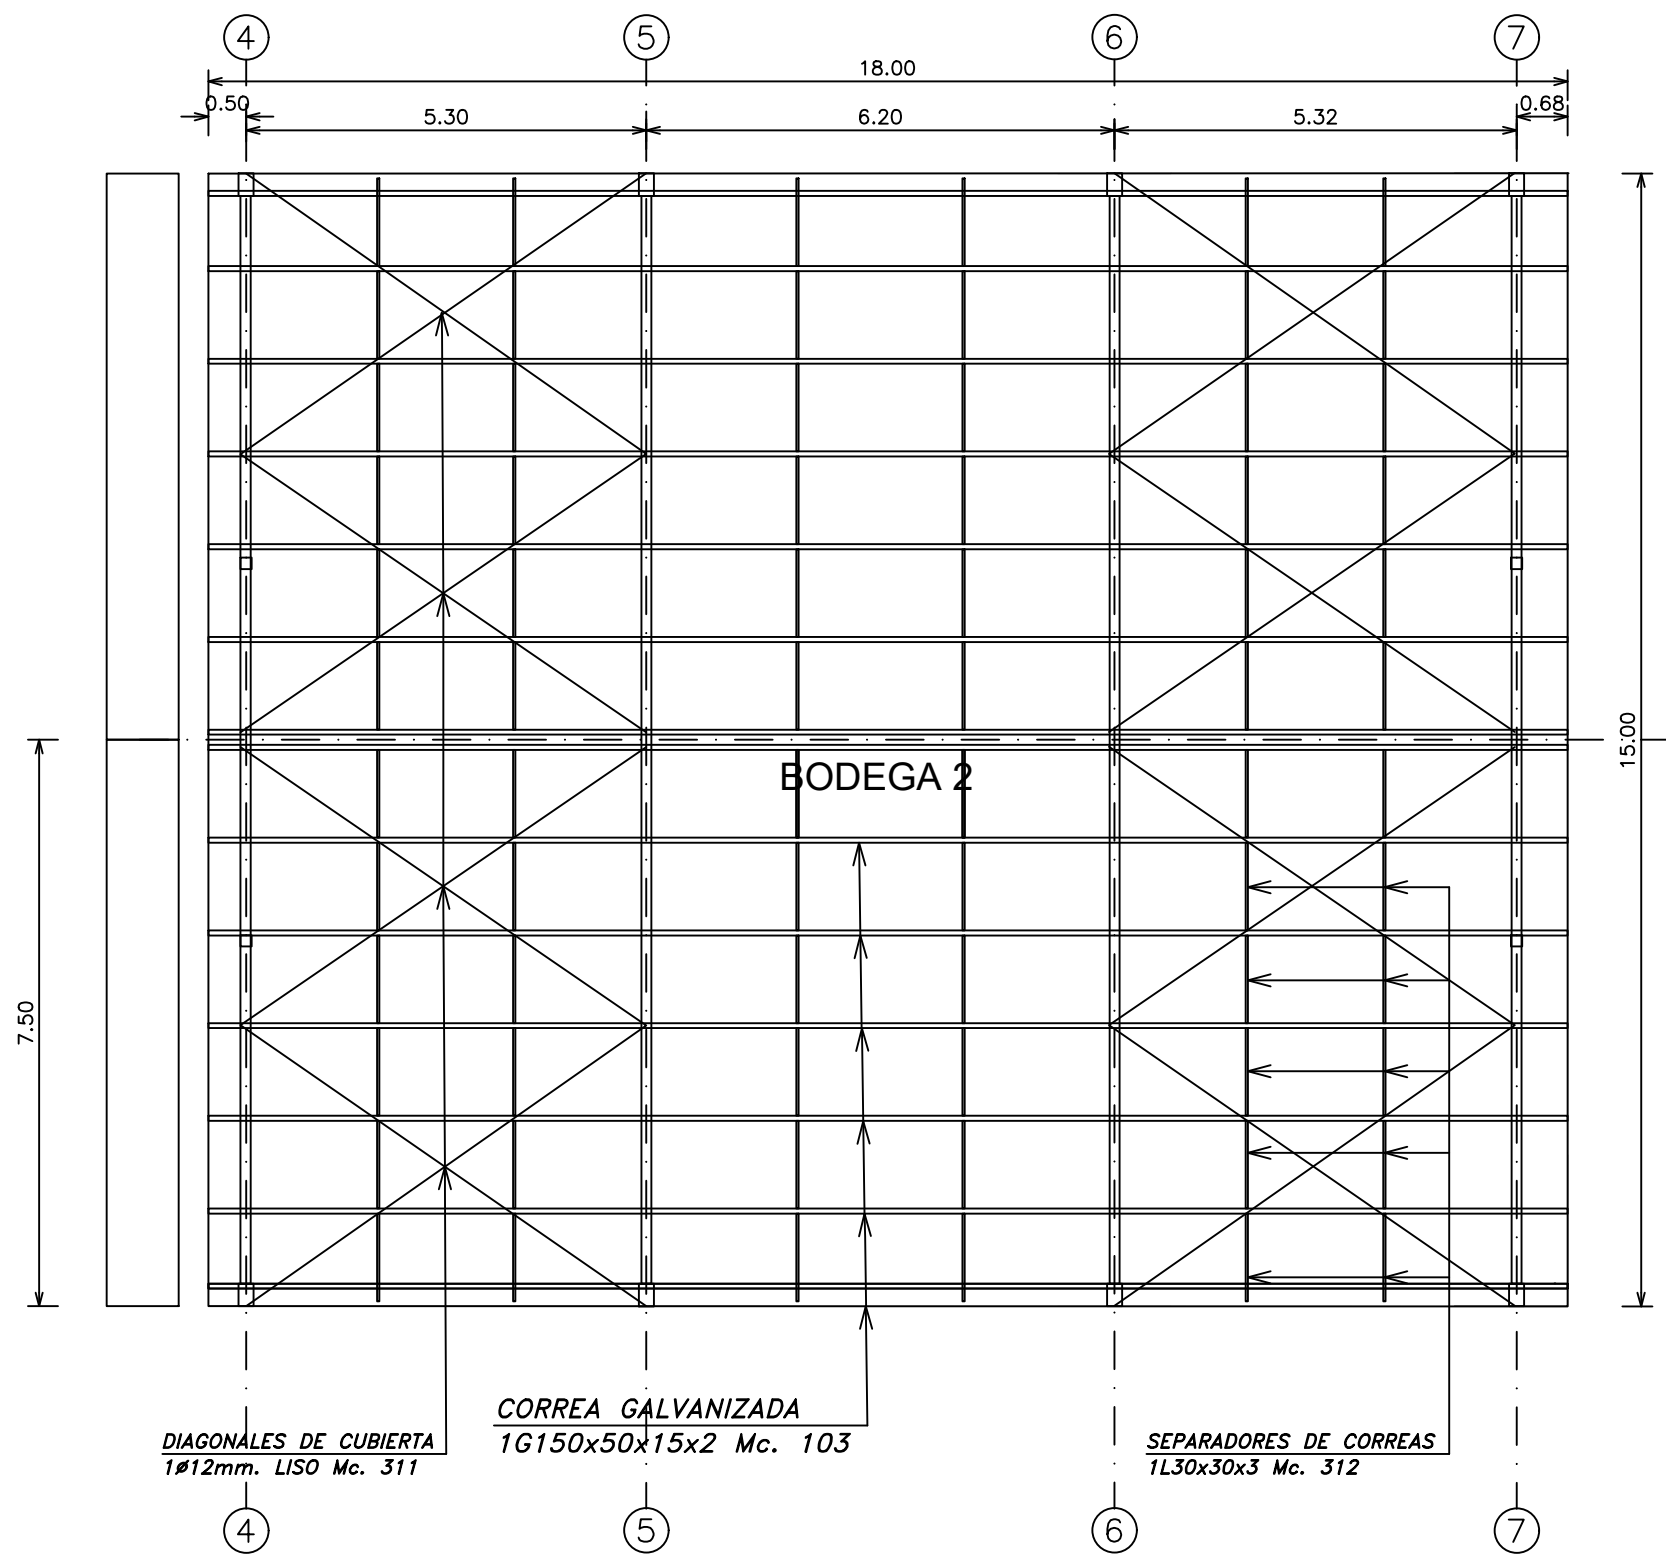


CUBIERTA BODEGA 2
Escala 1:100

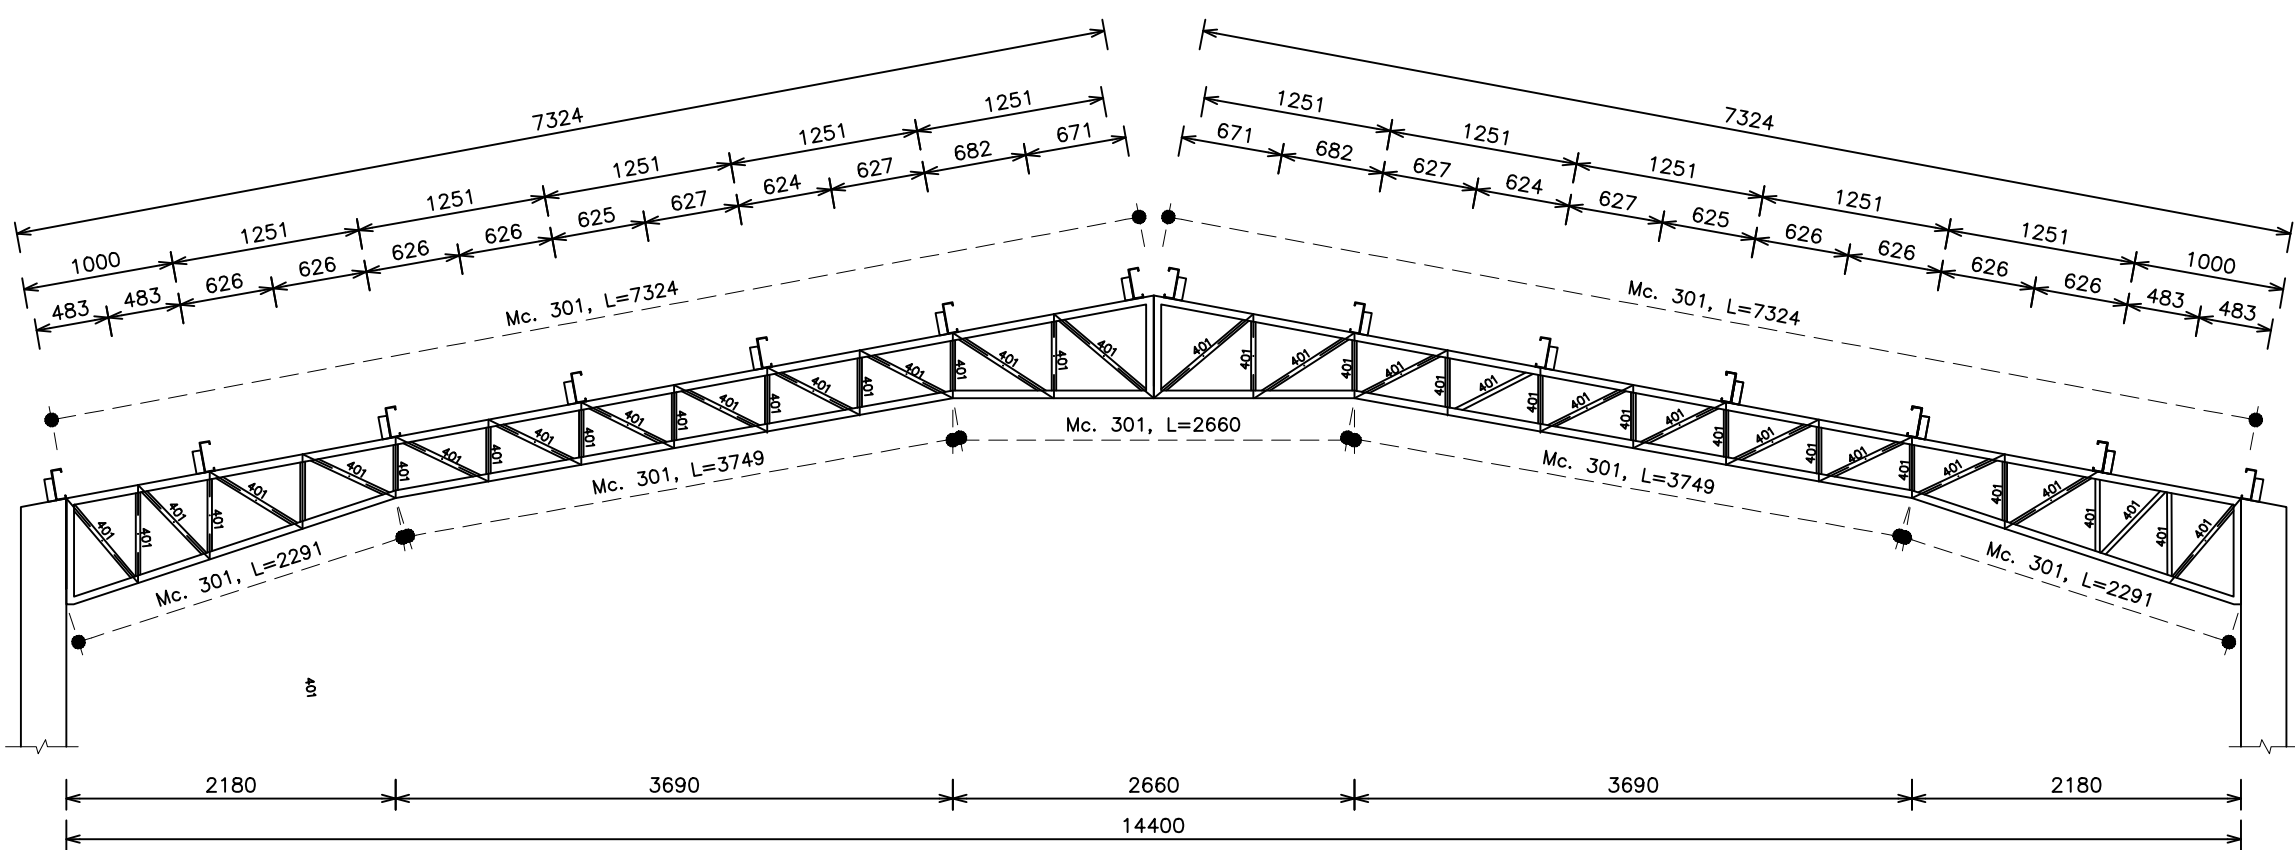


DETALLE DE VIGA TIPO 1
Escala 1:50


NOMENCLATURA		
Marca	Nro.	Perfiles
301	1	C 125 x 50 x 3
302	1	C 125 x 50 x 4
401	2	L 30 x 30 x 3
402	2	L 25 x 25 x 3

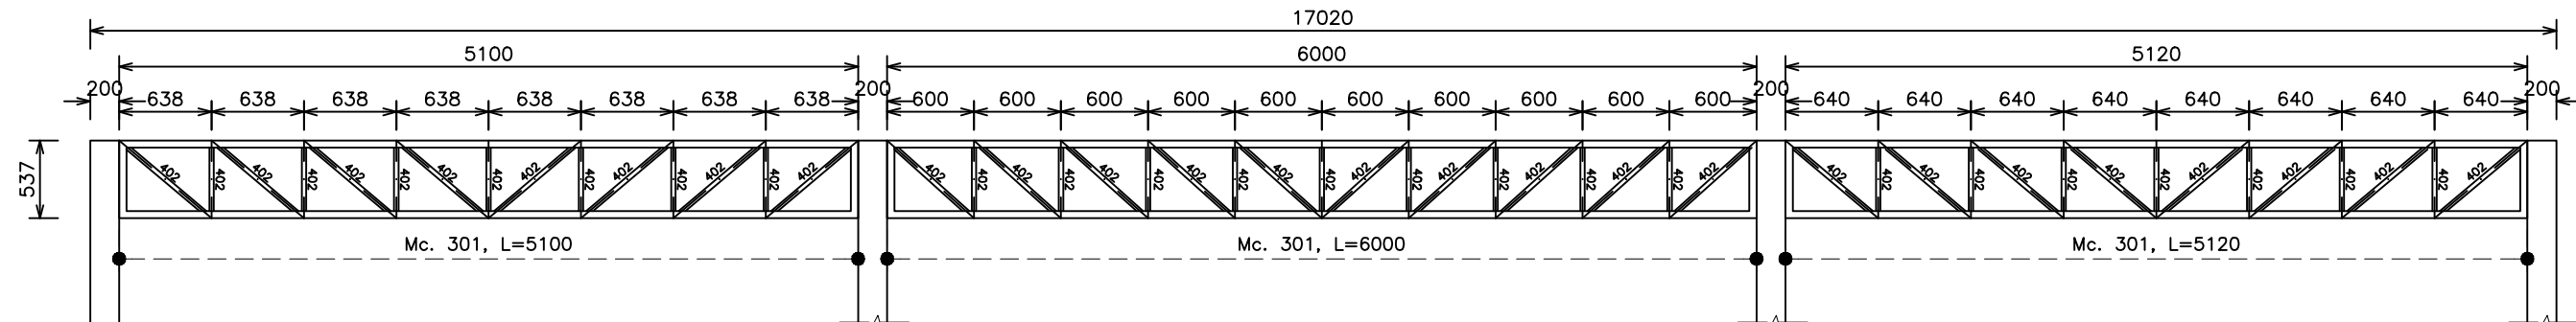



DETALLE DE VIGA TIPO 2
Escala 1:50

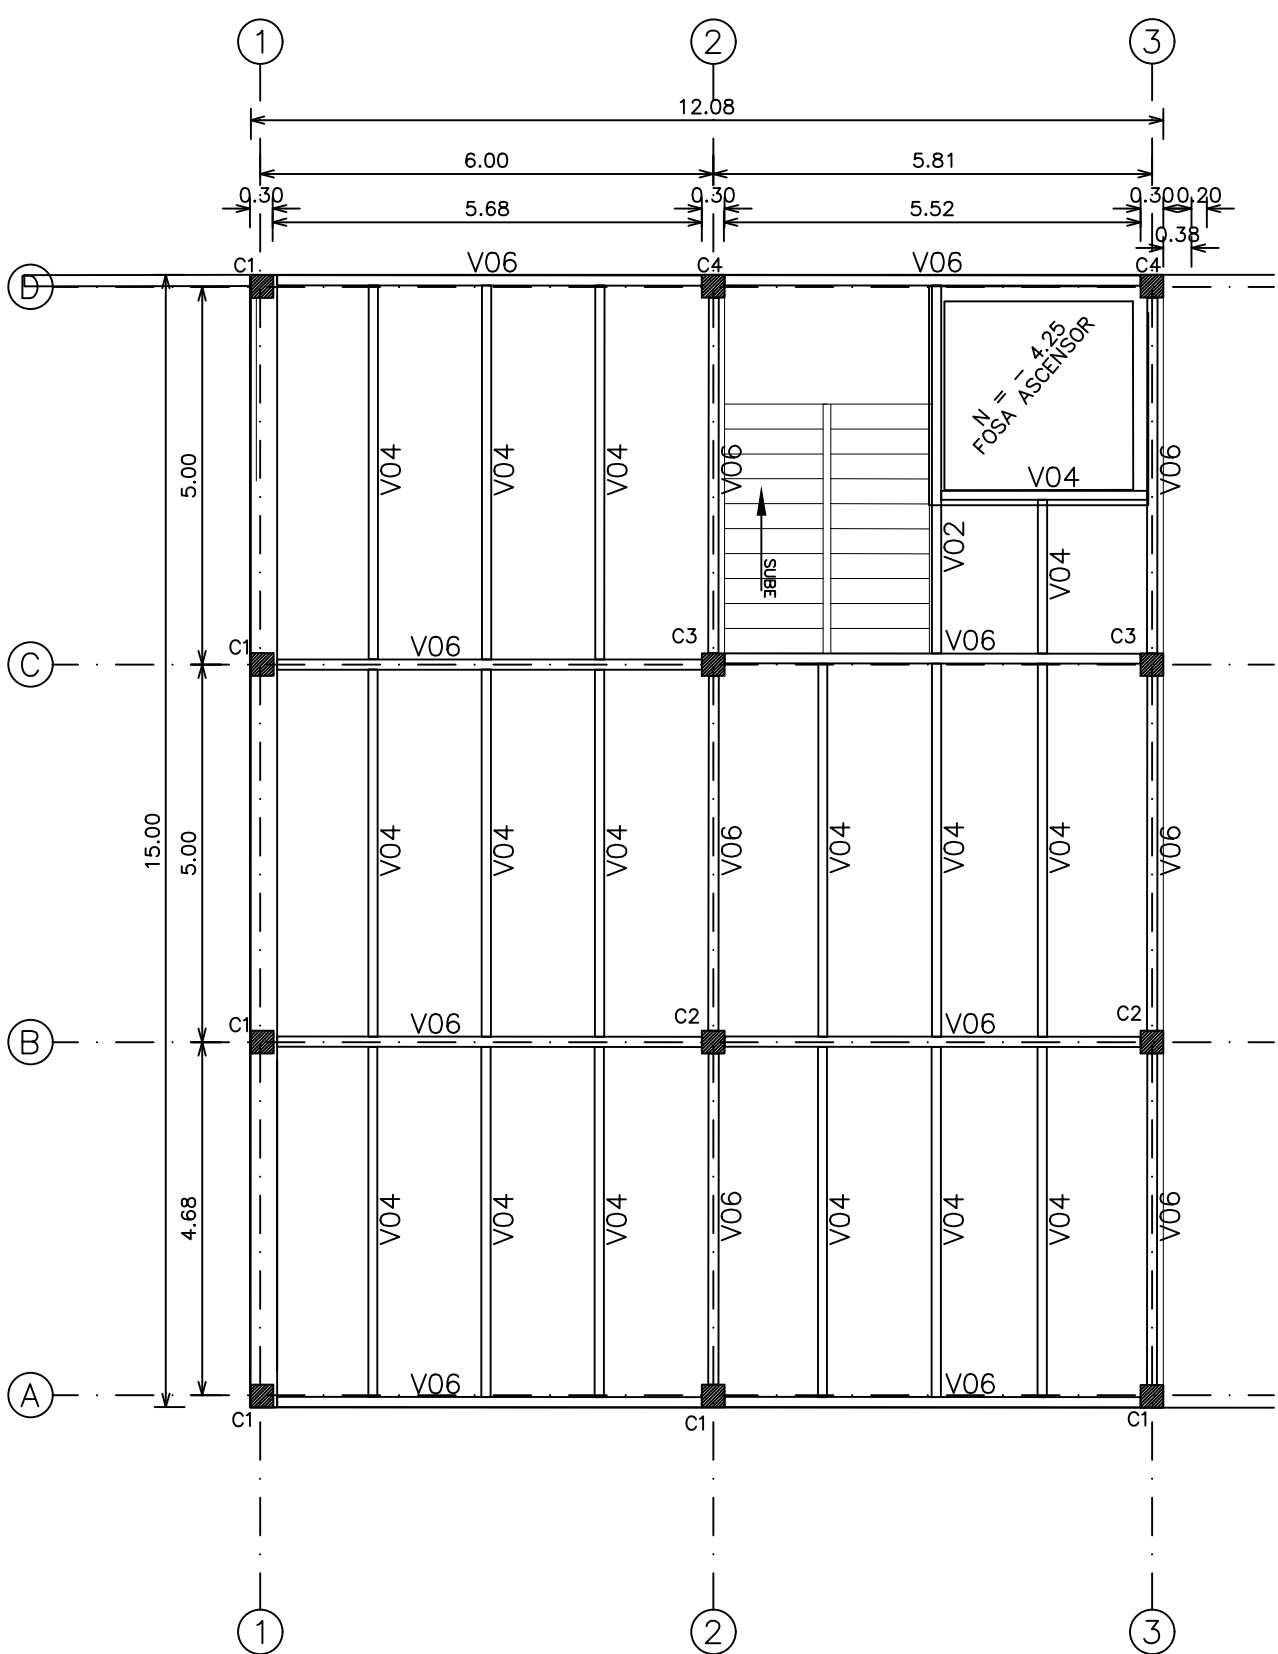

LOSA Nivel +0.00
Escala 1:100

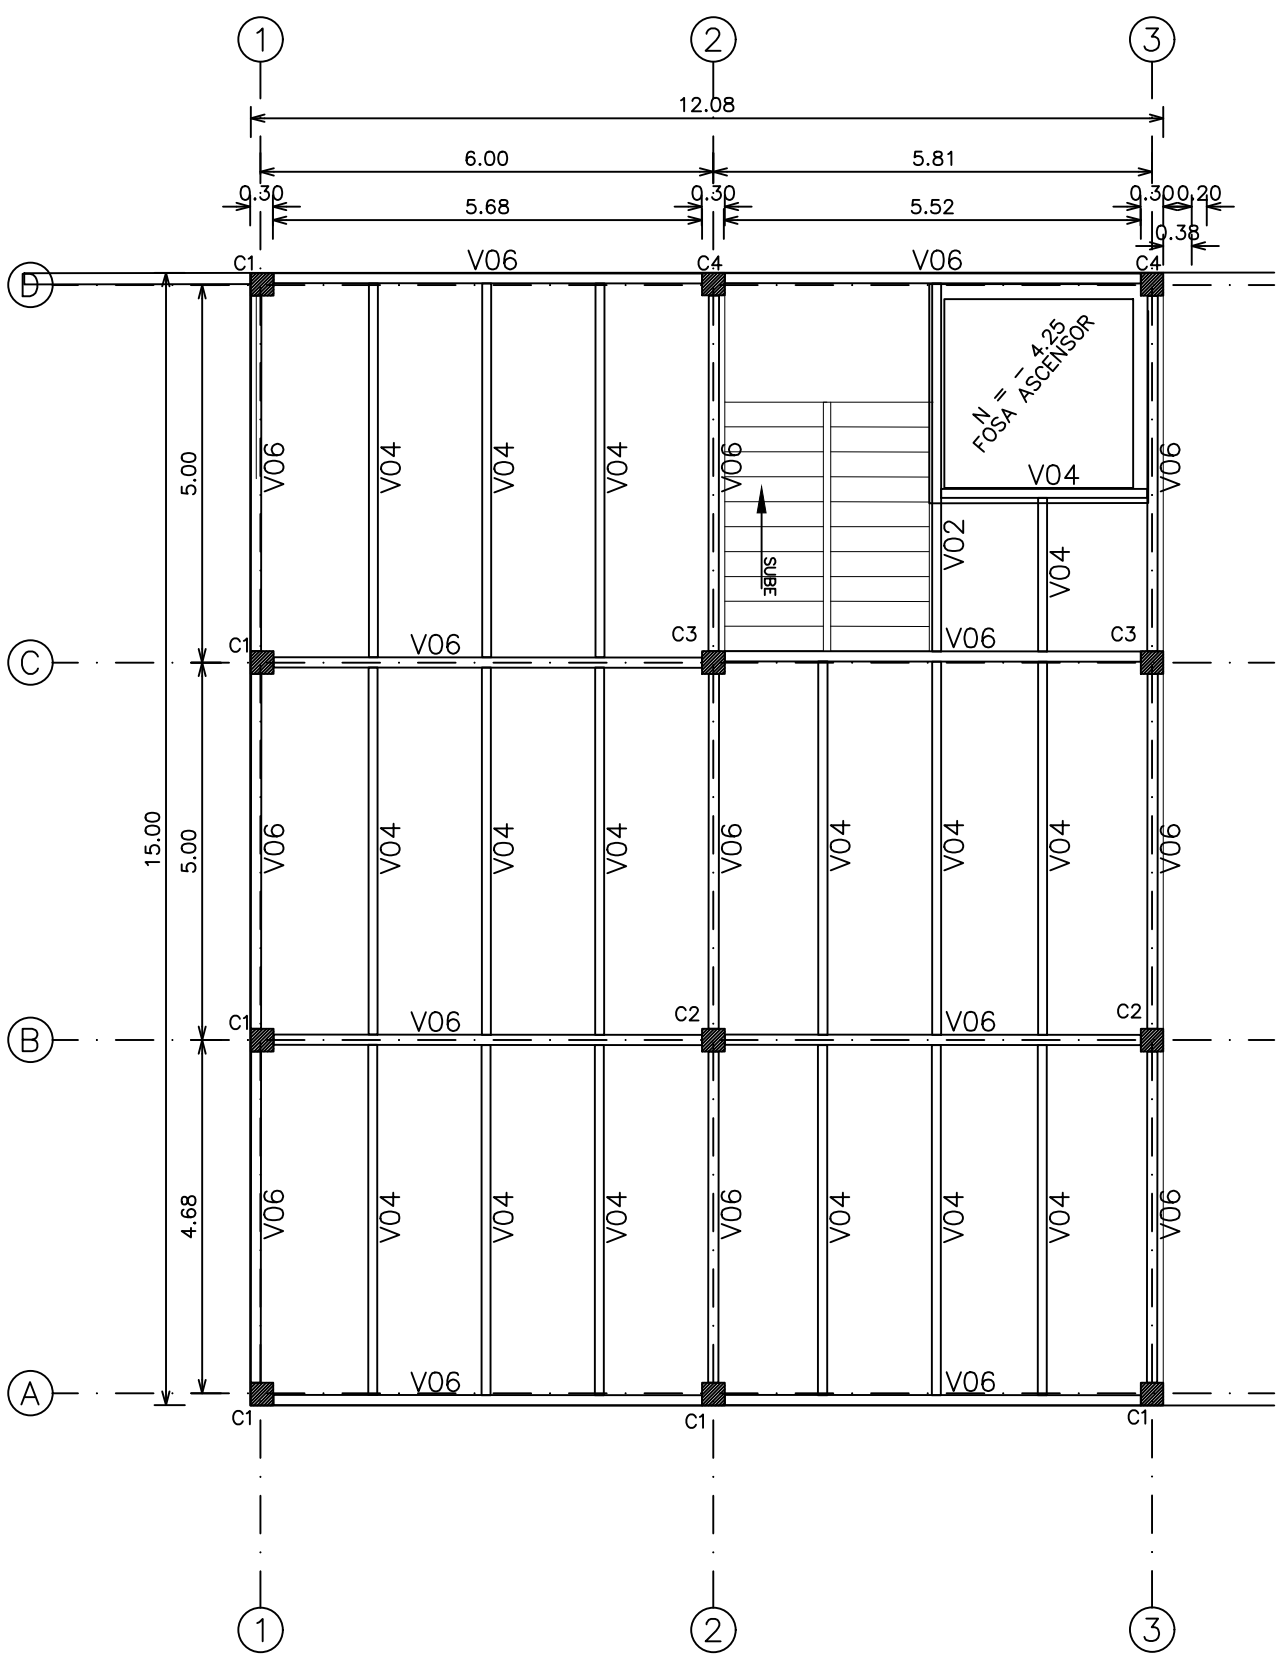

LOSA Nivel +3.40; +6.20
Escala 1:100

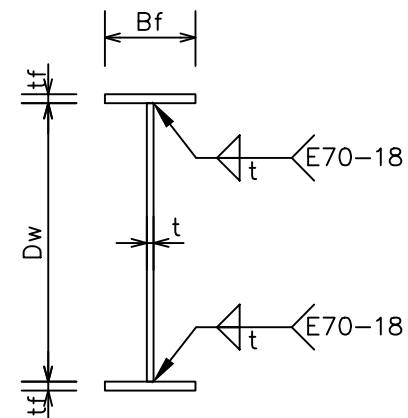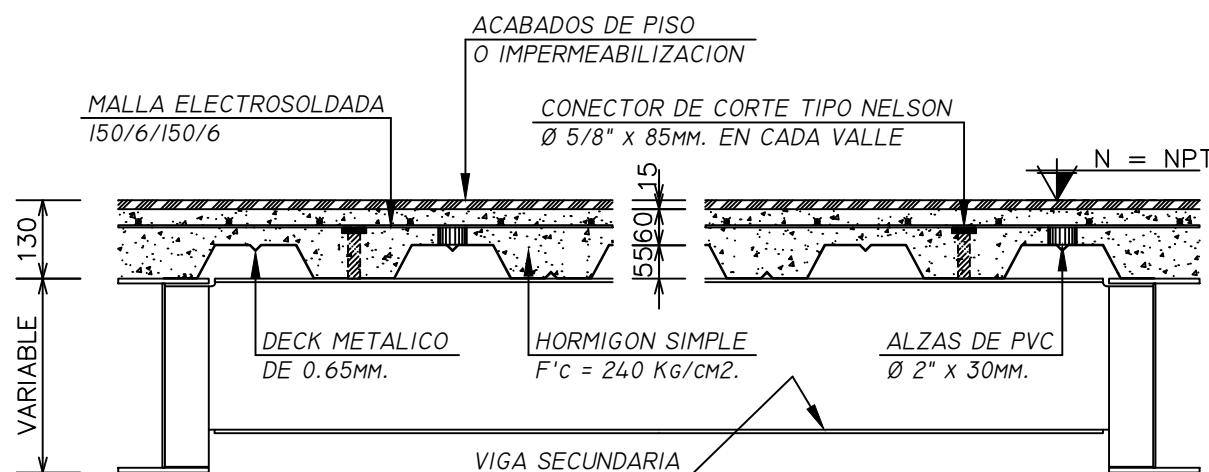

NOMENCLATURA DE VIGAS		
VIGA	MARCA	Dw . tw + Bf . tf
V02	200	250x4 + 120x8
V04	201	200x4 + 120x8
V06	202	300x4 + 135x8
V08	203	300x4 + 135x10

Especificaciones Técnicas de Cimentación

- RESISTENCIA CILINDRICA DEL HORMIGON SIMPLE $F'c=210 \text{ Kg/cm}^2$.
- LIMITE DE FLUENCIA HIERRO REDONDO CORRUGADO $Fy=4200 \text{ Kg/cm}^2$.
- LONGITUD MINIMA DE TRASLAP 40 DIAMETROS DE LA VARILLA.
- RECUBRIMIENTOS MINIMOS: CIMENTACION Y MUROS (3-5-7)cm. COLUMNAS Y VIGAS 3cm. CADENAS 2.5cm.
- TAMARO MAXIMO DEL AGREGADO GRUESO 3/4"
- RESISTENCIA ADMISIBLE DEL SUELO: SEGUN ESTUDIO 5 T/m².
- REPLANTILLO $F'c=180 \text{ Kg/cm}^2$.
- PLACAS DE APOYO GRADO ASTM 572 A-50 ksi.

Tipos de Hierro Corrugado

PROYECTO BODEGAS FARINANGO

REPRESENTANTE LEGAL:

A.
CC.
PROPIETARIO:

PROFESIONAL:

ING. KARINA F. PANAMÁ QUIZHPI
REG. SENESCYT: 1001-2022-2433832
CC: 1723966071

UBICACION:

PREDIO:

FECHA: JULIO-2026
DISEÑO: ING. KARINA PANAMÁ
DIBUJO: ING. KARINA PANAMÁ
ESCALA: INDICADA

CONTIENE:
CIMENTACIÓN

LAMINA:
A-2

SELLOS MUNICIPALES